


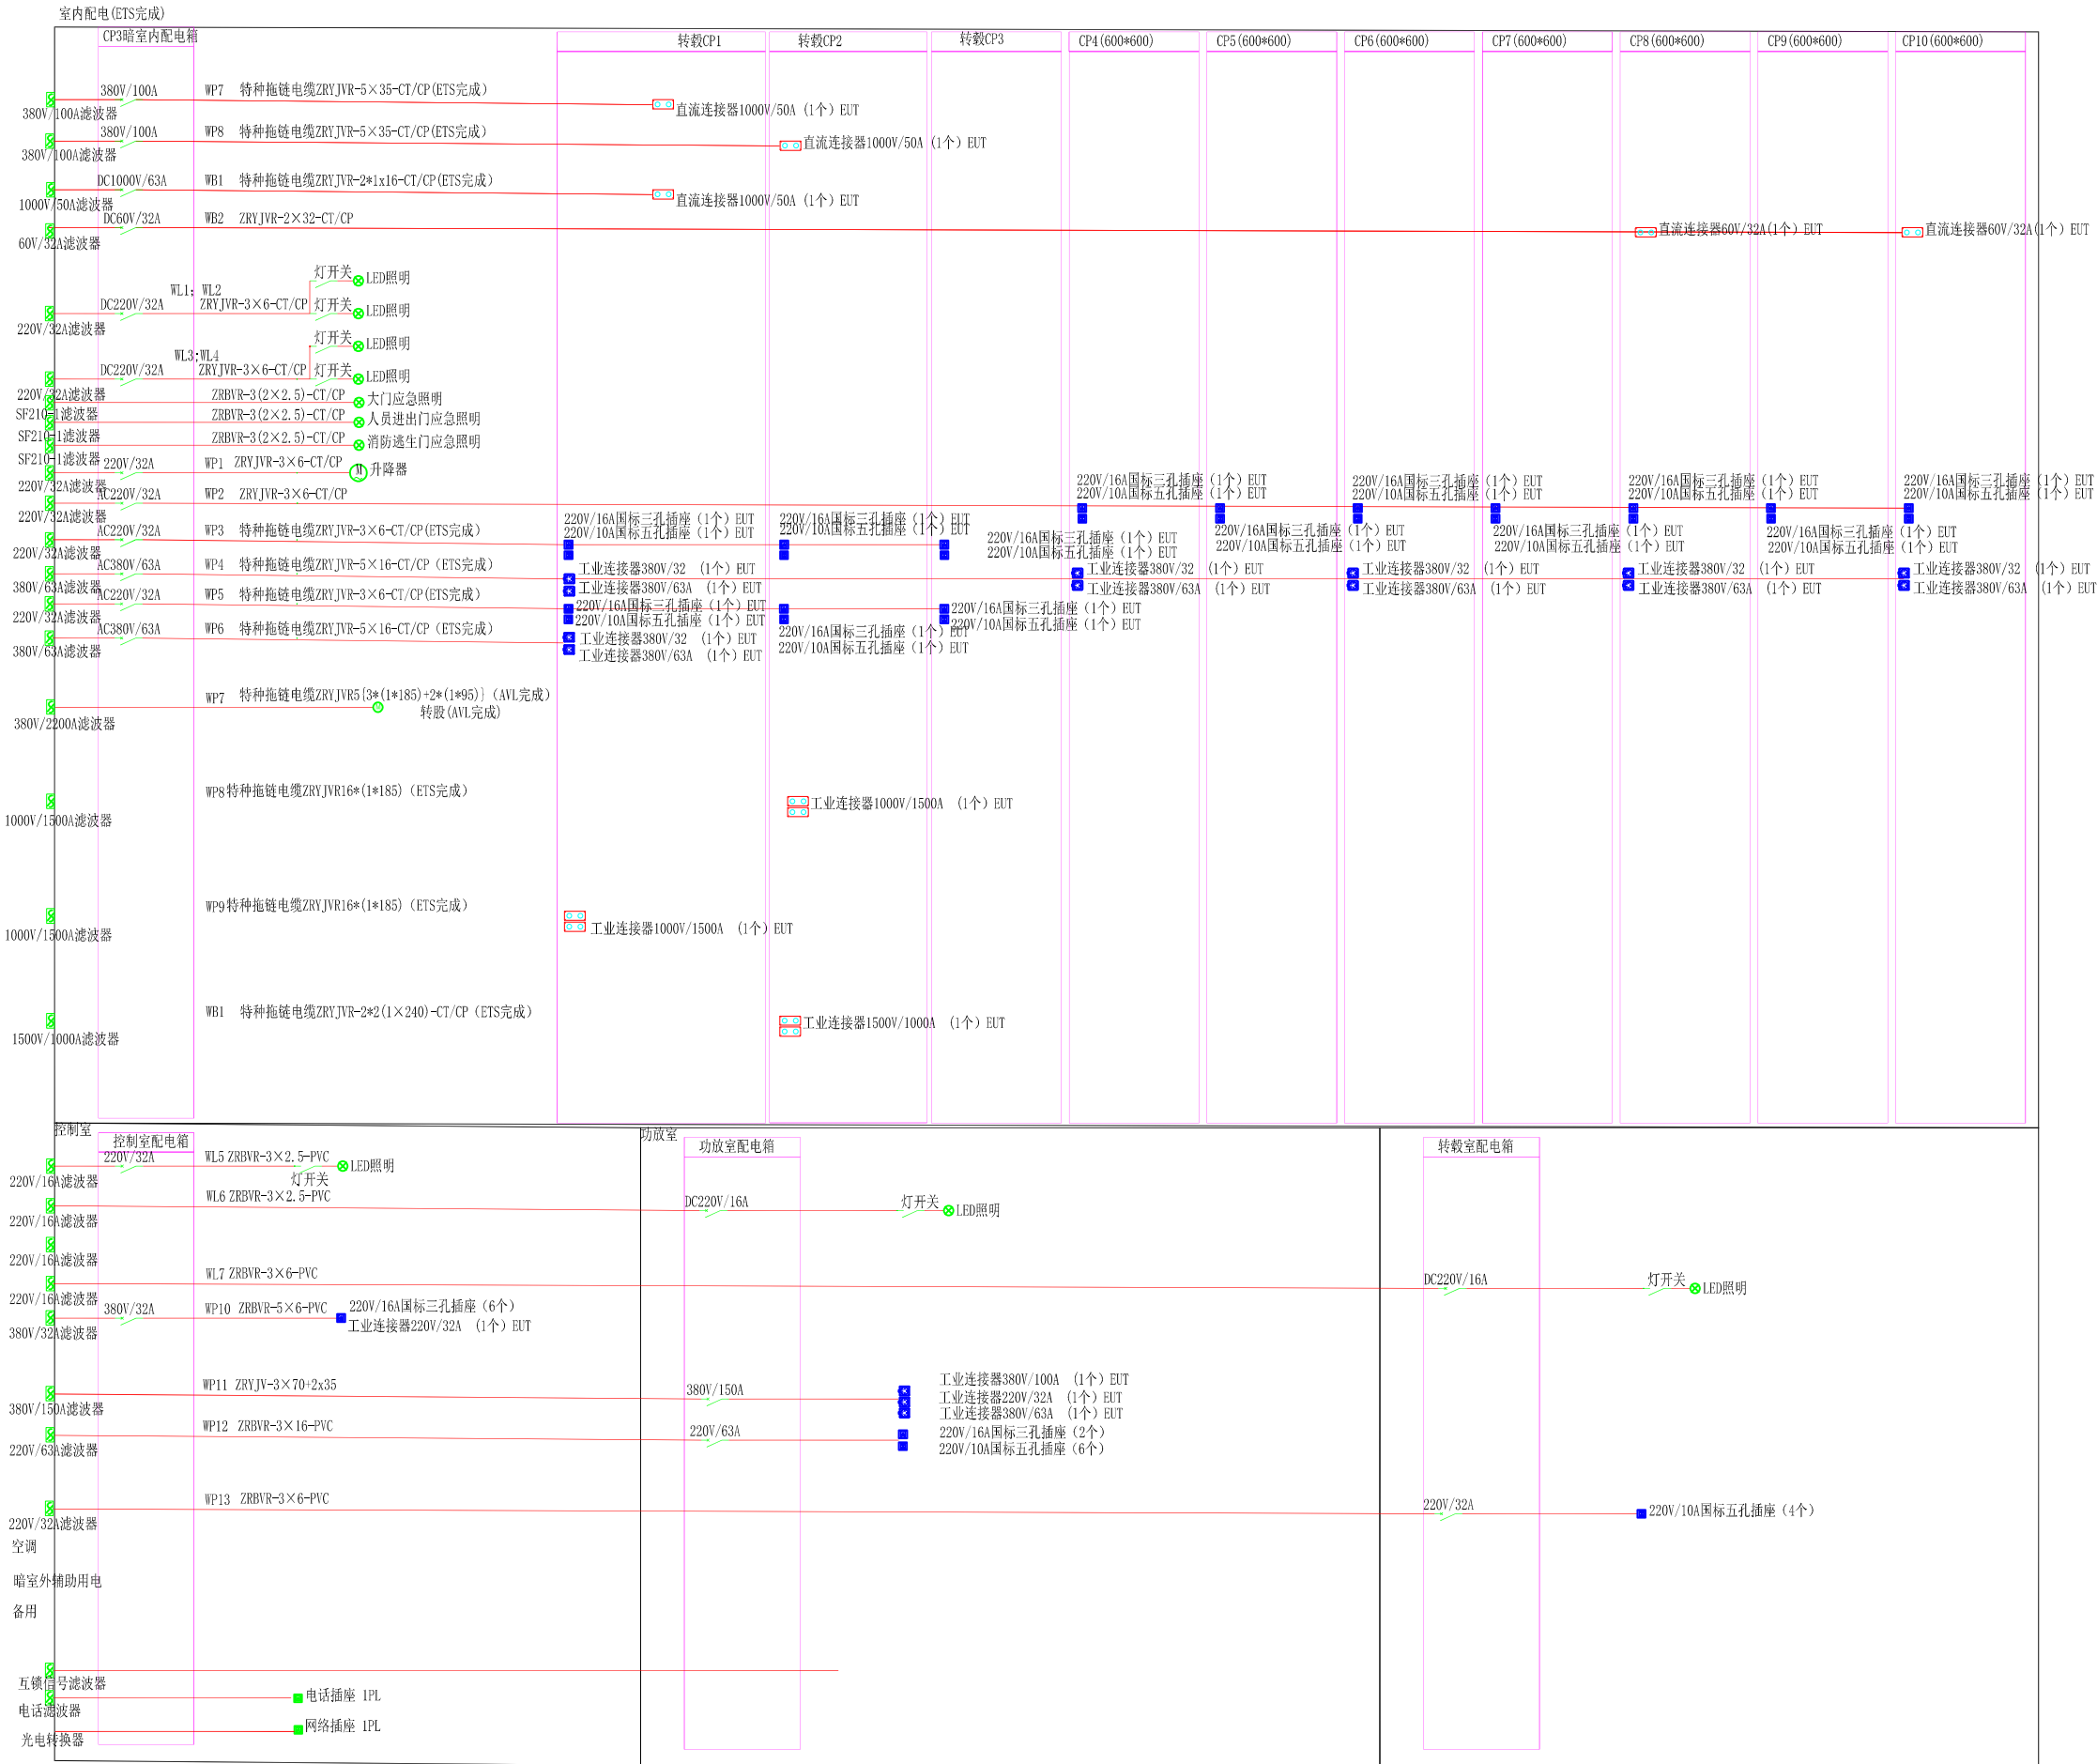

ETS·LINDGRENTM

CHINA

An ESCO Technologies Company

Beijing Lingren E.M. Technology Co.,Ltd.

China Office :
No. 17 Madian East Road, Haidian Dist., Beijing, P.R.C
Beijing P.R.C100083
Tel:8610-82730877 Fax:8610-82730880

整车设备室内配电系统图

姓名: SHEET TITLE

This document and the information contained therein are the property of LINDGREN RF ENCLOSURES, INC. Glendide Heights, Illinois. Recipient agrees NOT to:
(1) Use such information for purposes other than those expressly authorized by LINDGREN RF ENCLOSURES, INC.
(2) Reproduce or copy this document without the express written permission of LINDGREN RF ENCLOSURES, INC.
(3) Reproduce or copy this document either in whole or in part without the express written permission of LINDGREN RF ENCLOSURES, INC.

版本	描述

工程名称	项目

制图人: Zhang Haipeng

审核人:

检查人:


负责人:


客户:

日期: 10-03-2025 比例: NONE

方案 E

图纸编号: E1.2

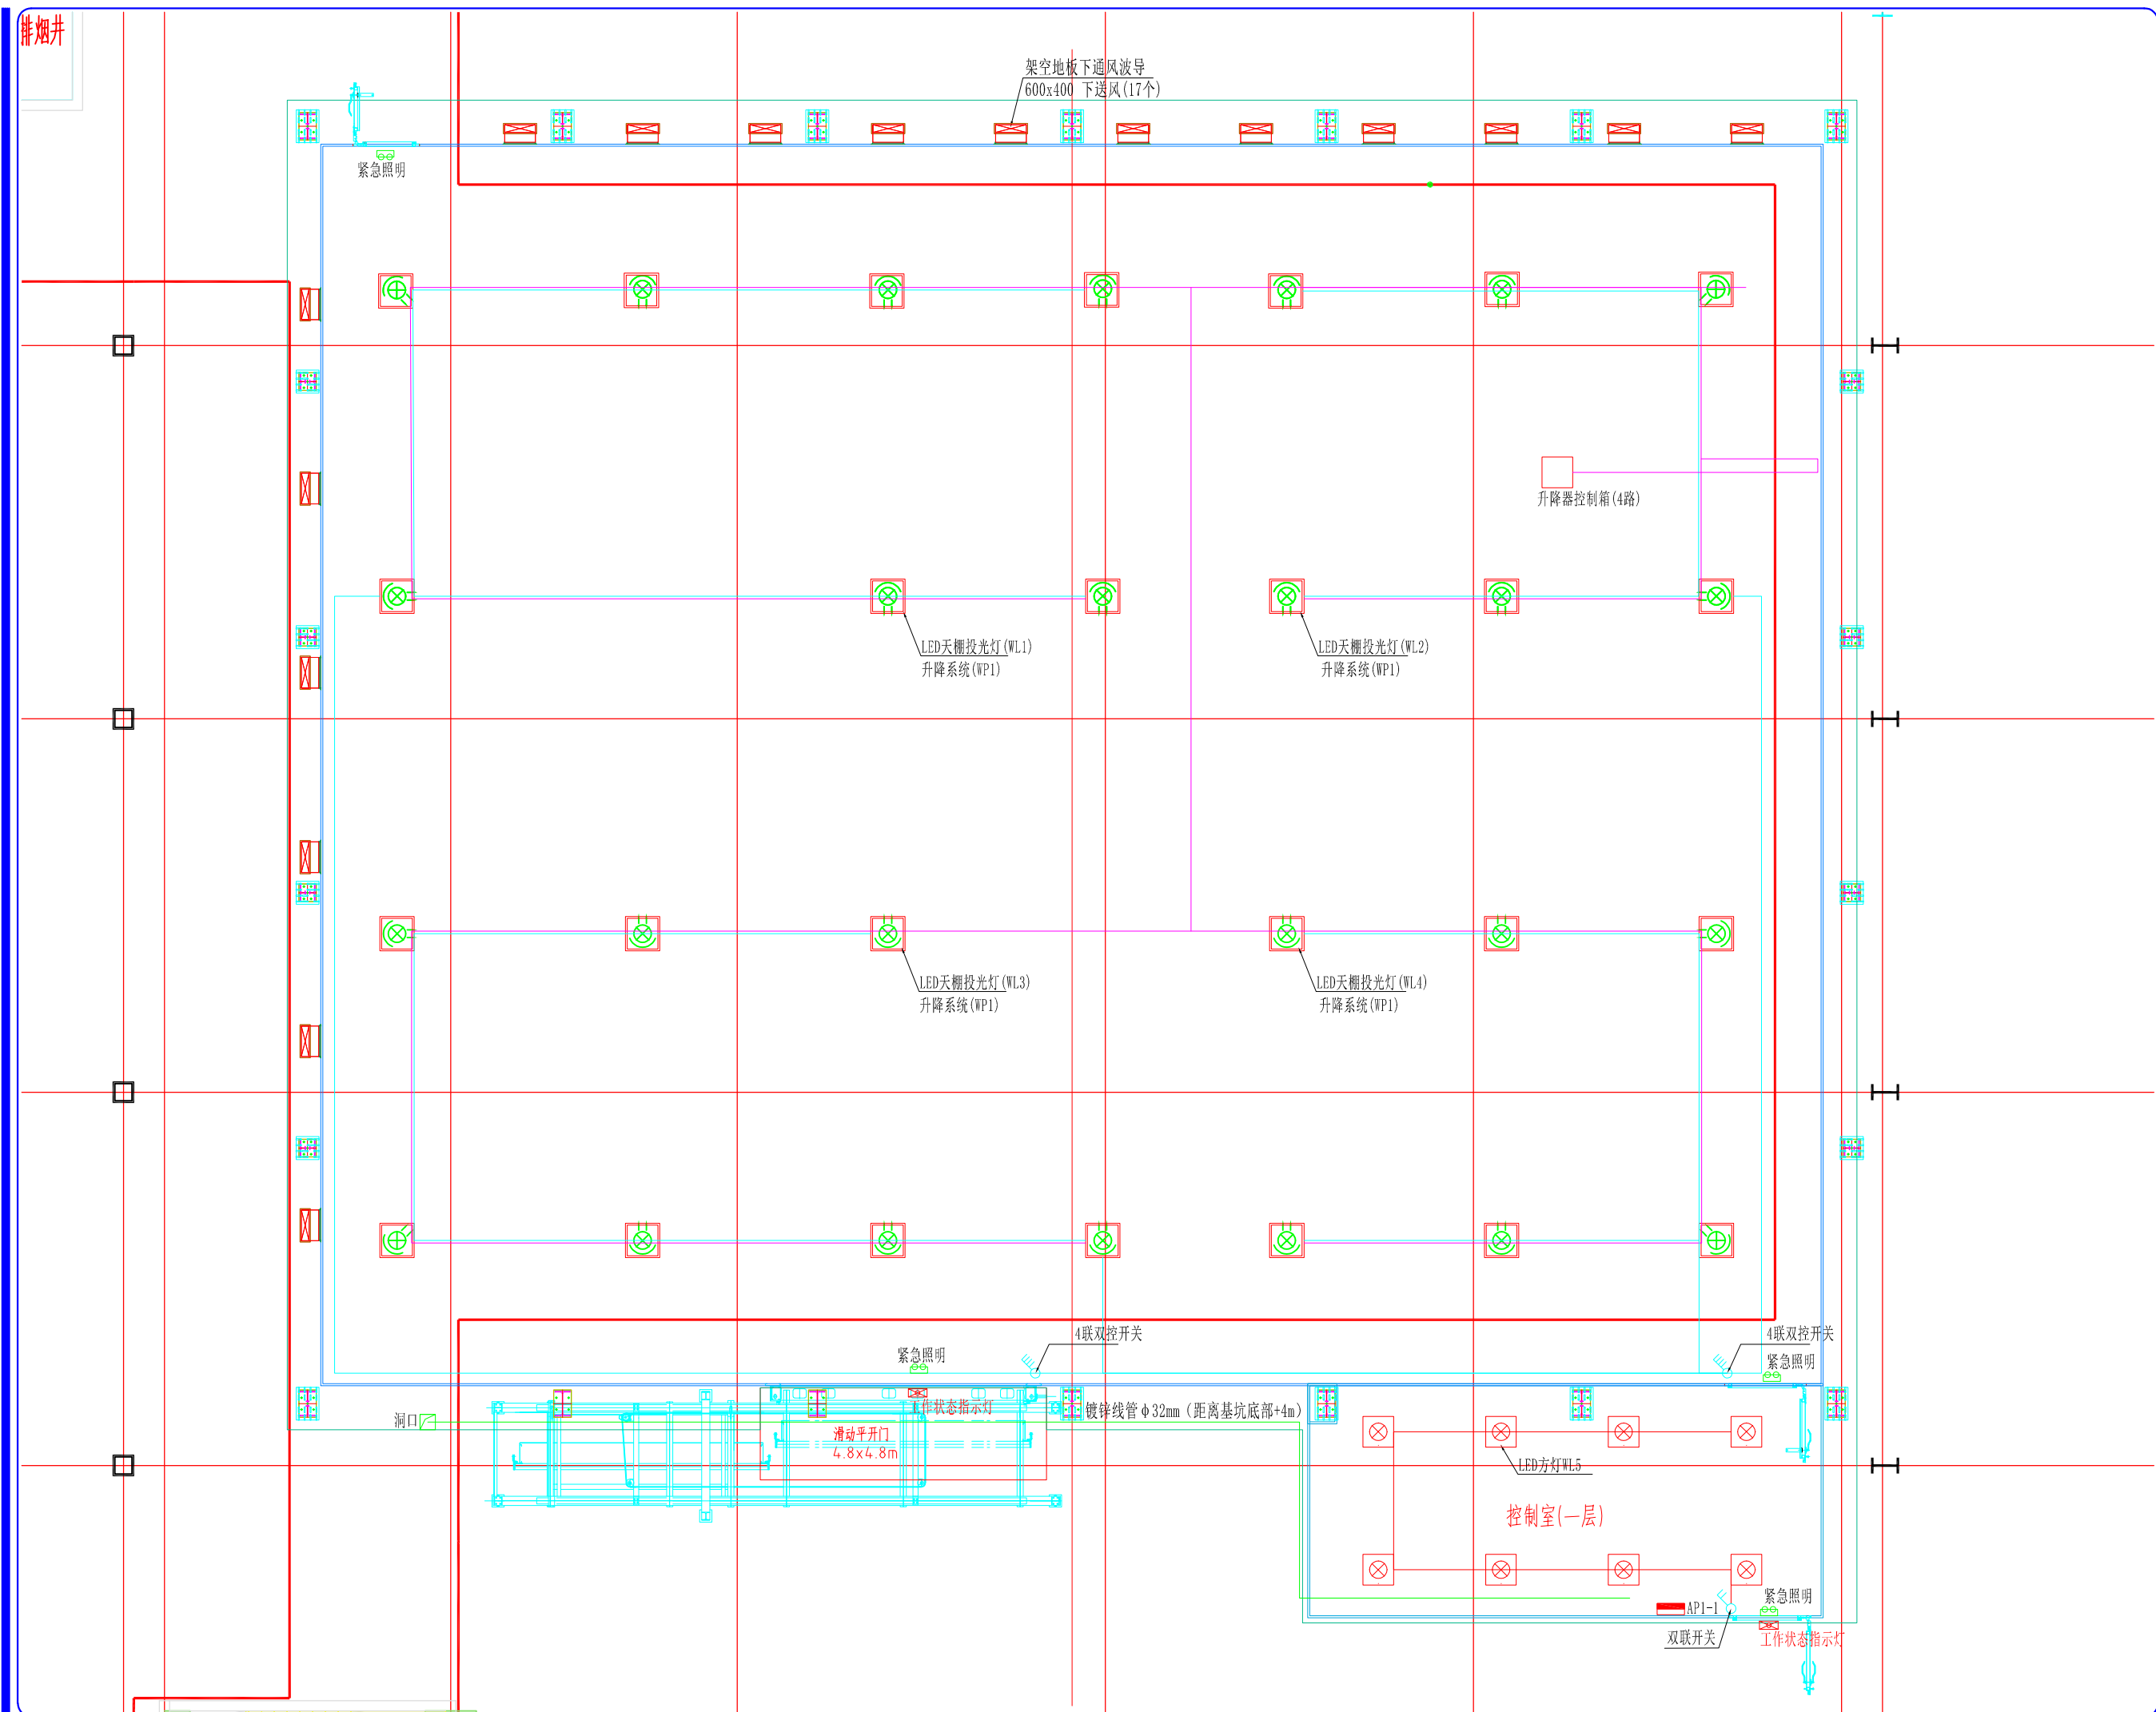

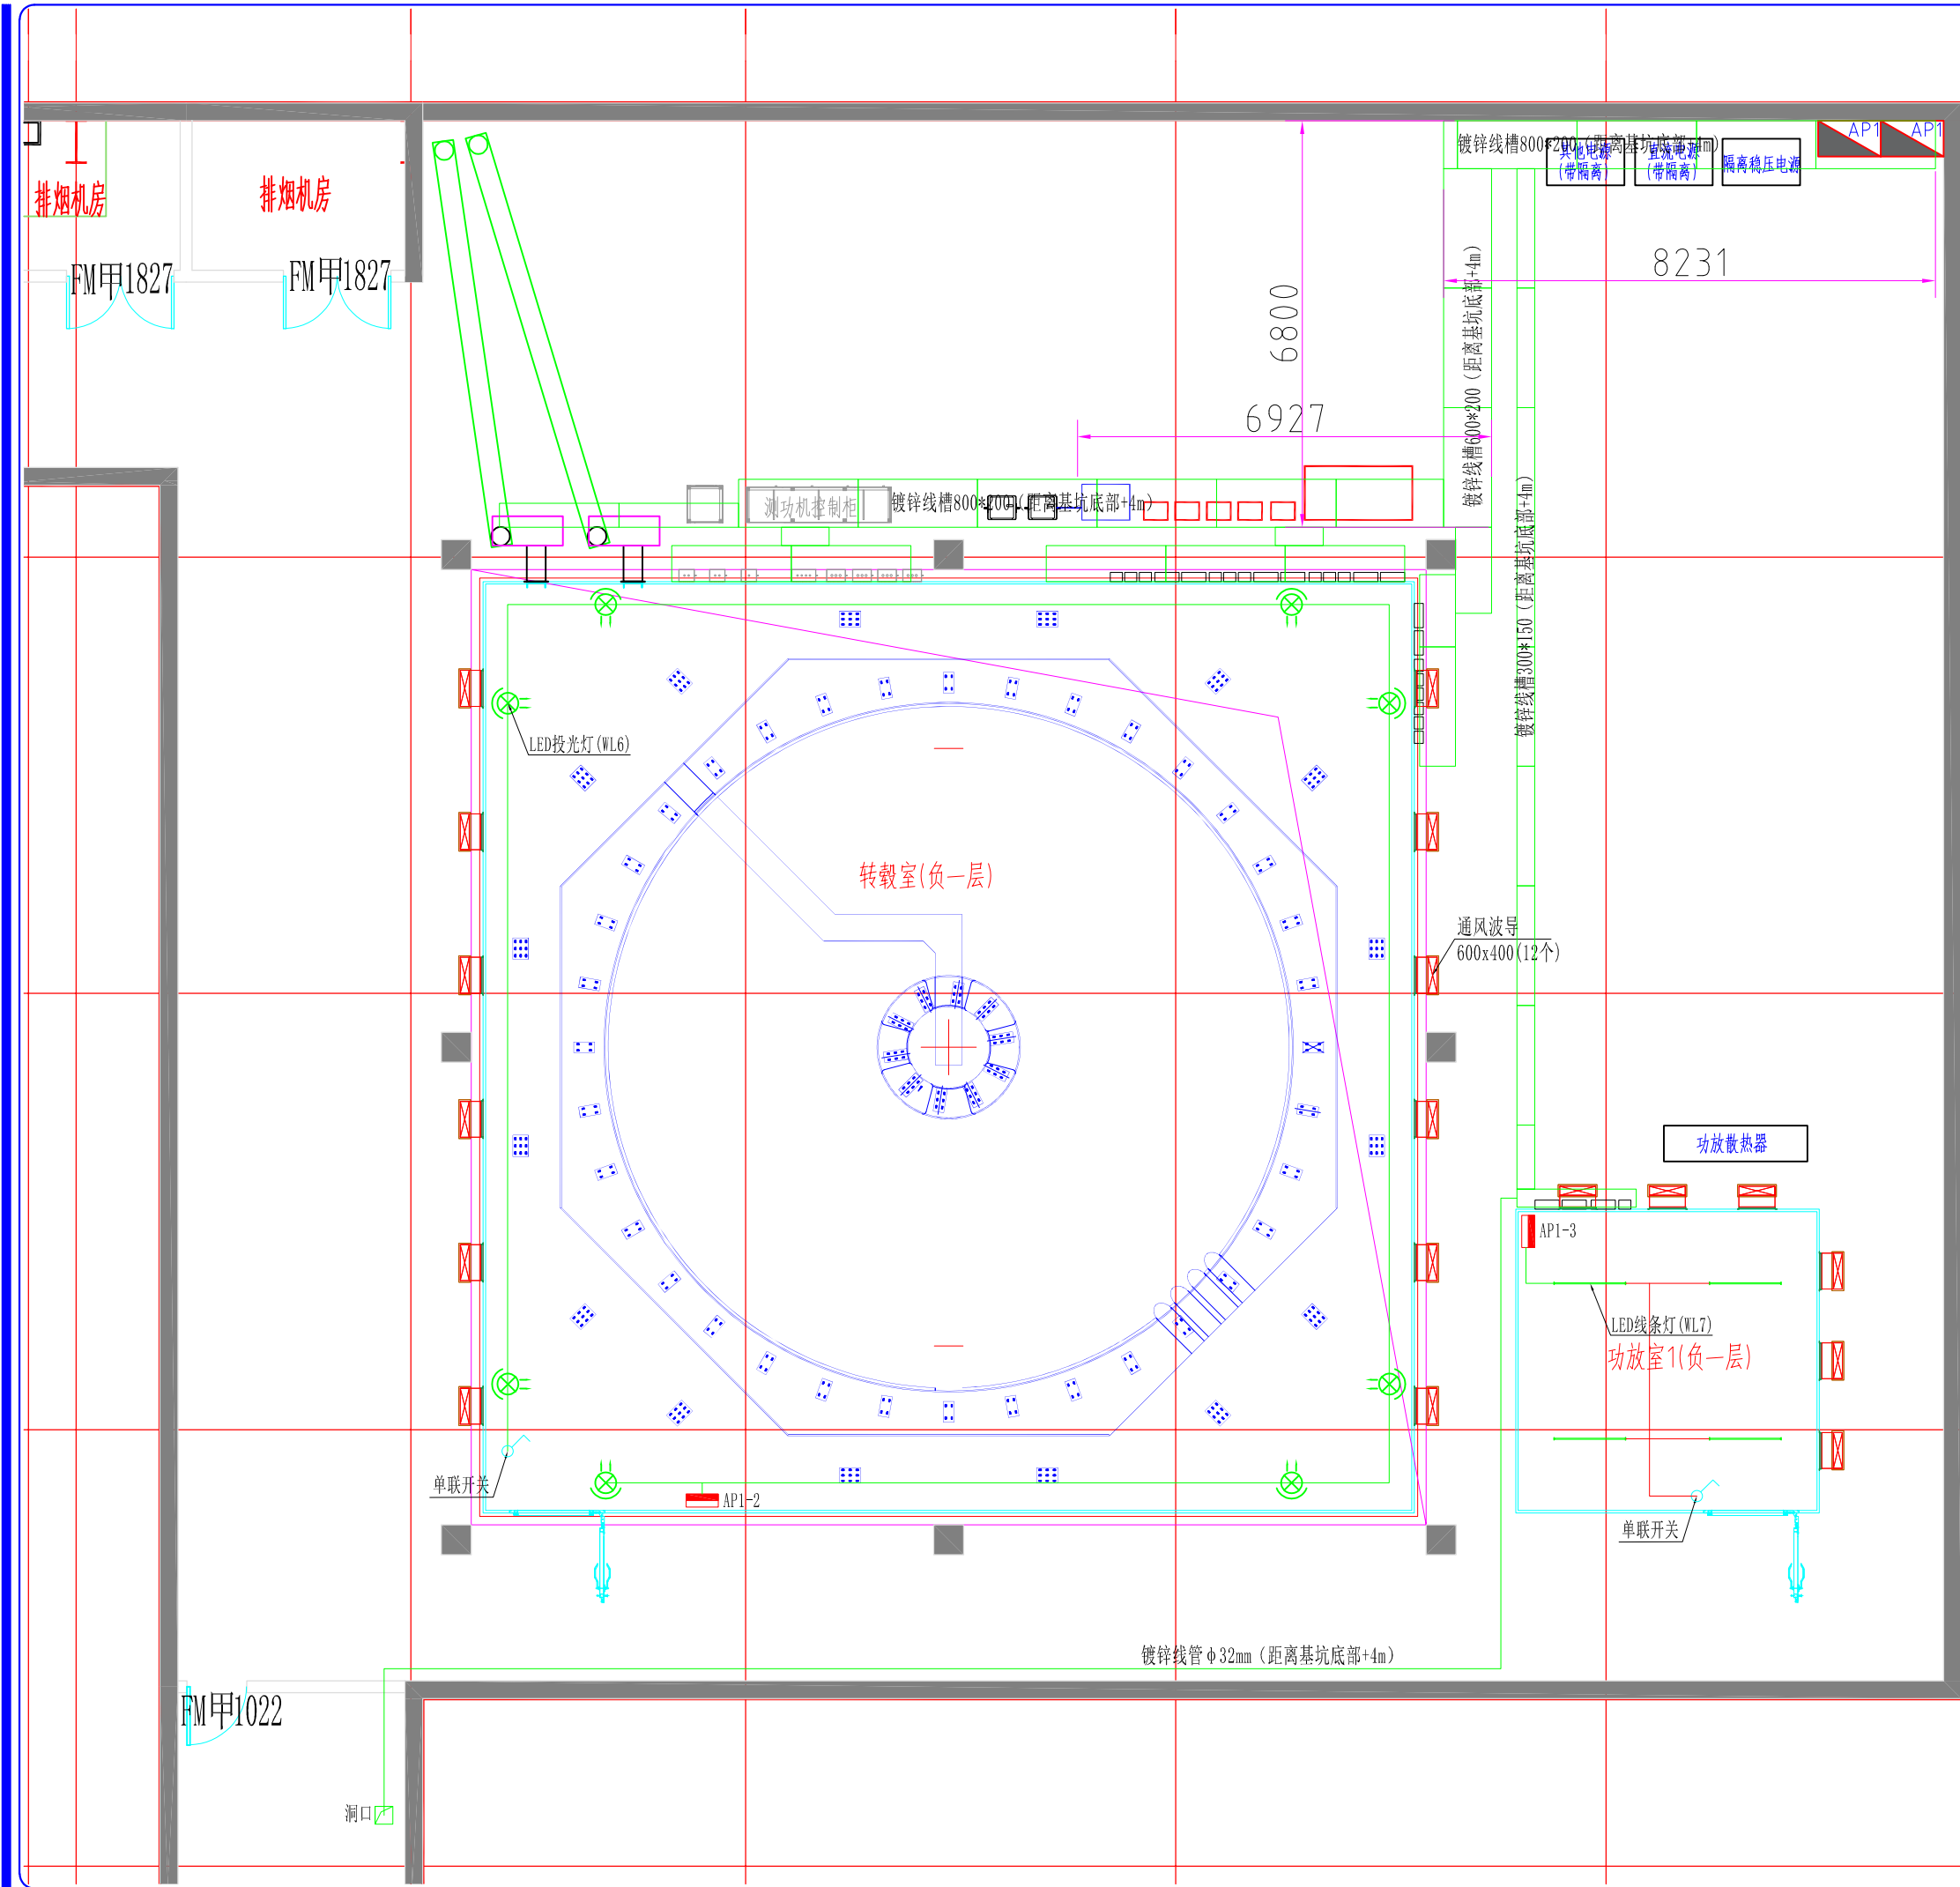

ETS·LINDGRENTM

CHINA

An ESCO Technologies Company

Beijing Lindgren E.M. Technology Co., Ltd.

China Office :
No. 17 Madian East Road, Haidian Dist., Beijing, P.R.C
Beijing P.R.C100083
Tel: 8610-82730877 Fax: 8610-82730880

转毂室&功放室照明布局图

图名: SHEET TITLE

转毂室&功放室照明布局图

This document and the information contained therein are the property of LINDGREN RF ENCLOSURES, INC. Glendale Heights, Illinois. Recipient agrees NOT to:
(1) Use such information for purposes other than those expressly authorized by LINDGREN RF ENCLOSURES, INC.
(2) Reproduce, in any form, or by any means, electronic, mechanical, photocopying, recording, or by any information storage and retrieval system, without the express written permission of LINDGREN RF ENCLOSURES, INC.
(3) Reproduce or copy this document either in whole or in part without the express written permission of LINDGREN RF ENCLOSURES, INC.

版本/日期	描述	设计	审核
1.0	转毂室&功放室照明布局图		

项目名称: PROJECT TITLE

NAST10m转毂室&OTA转毂室项目

地址: ADDRESS

制图人: DRAWN BY

Zhang Haipeng

审核人: CHECKED BY

负责人: MANAGER

客户: CUSTOMER

日期: DATE

10-03-2025

比例: SCALE

NONE

工号: JOB NO.


方案

版本: REV.

E

图纸编号: DRAWING NO.

E3

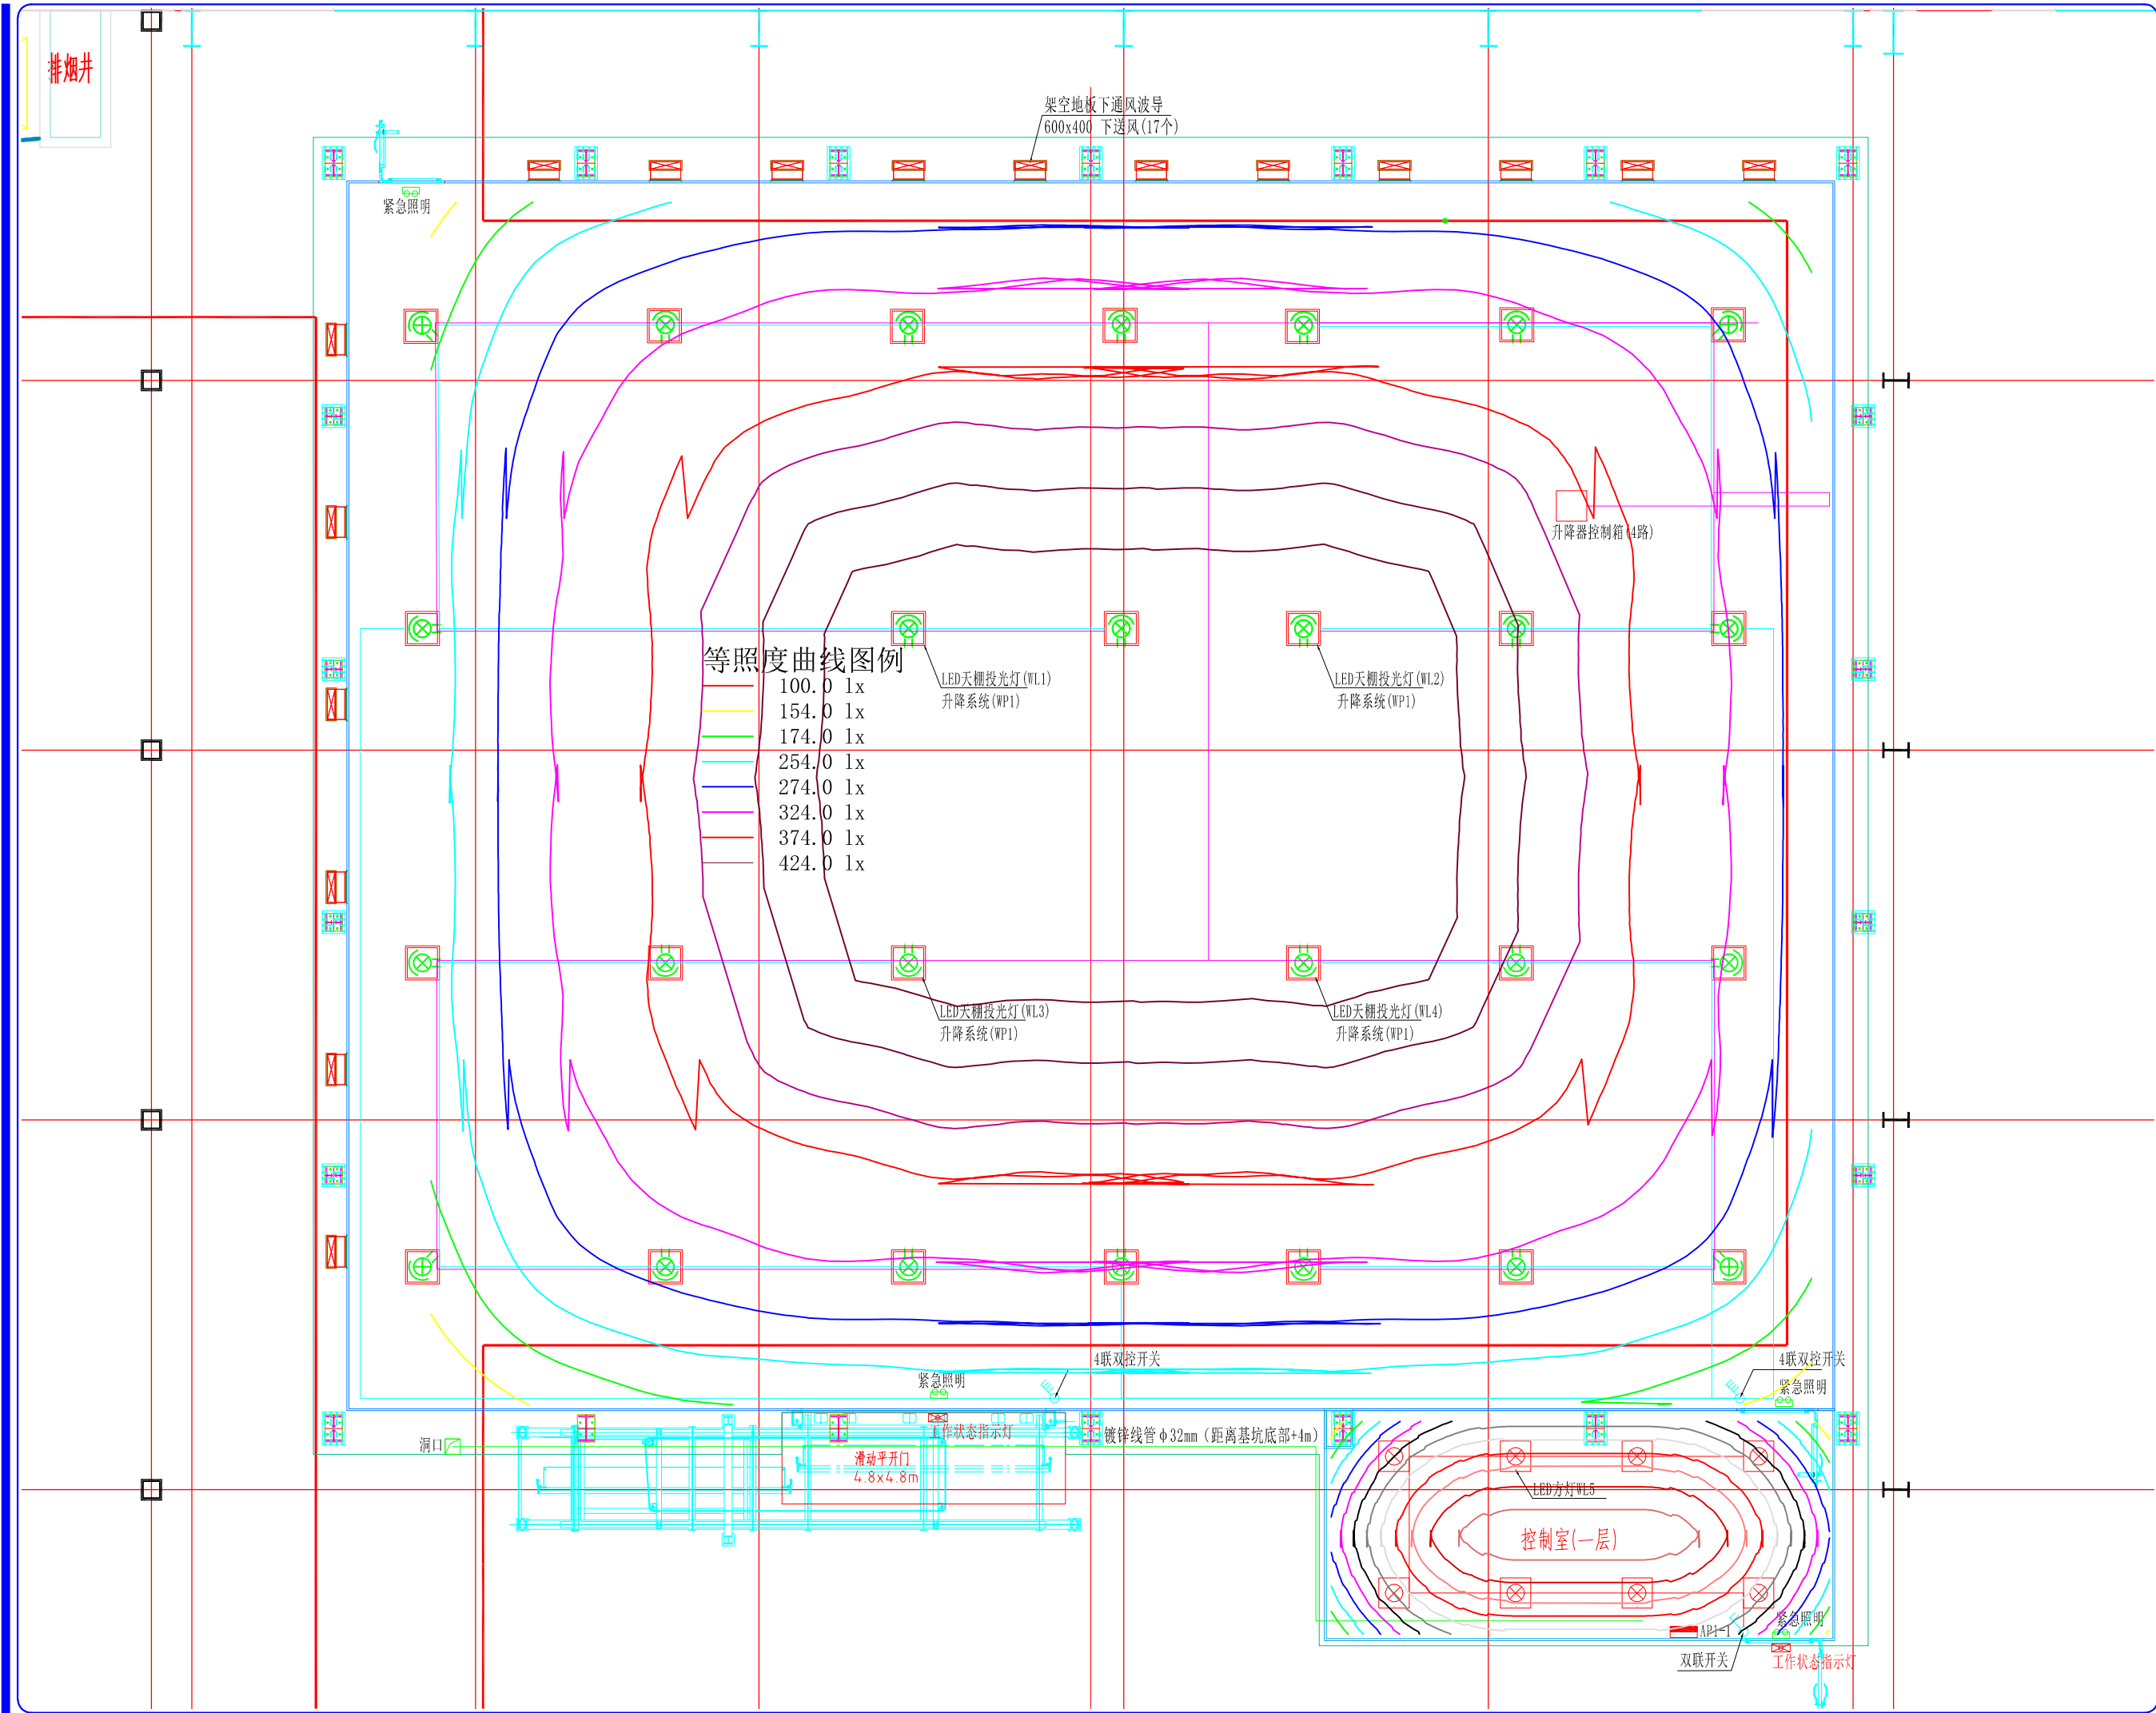



ETS-LINDGRENTM
CHINA
An ESCO Technologies Company
Beijing Lindgren E.M. Technology Co., Ltd.

China Office :
No. 17 Madian East Road, Haidian Dist., Beijing, P.R.C
Beijing P.R.C100083
Tel: 8610-82730877 Fax: 8610-82730880

图名:
SHEET TITLE

转觀室&功放室照度布局图

此文档和信息包含 therein 是 LINDGREN RF ENCLOSURES, INC. 的财产。接收人不得将此信息用于任何目的，除非事先获得 LINDGREN RF ENCLOSURES, INC. 的书面许可。接收人不得将此信息复制或传播，除非事先获得 LINDGREN RF ENCLOSURES, INC. 的书面许可。接收人不得将此信息用于任何目的，除非事先获得 LINDGREN RF ENCLOSURES, INC. 的书面许可。


版本/描述	日期	作者

工程名称	客户

制图人:	张海鹏
审核人:	
检查人:	
负责人:	
客户:	
日期:	10-03-2025
比例:	NONE

方案	E
----	---

图例编号:	E4
-------	----

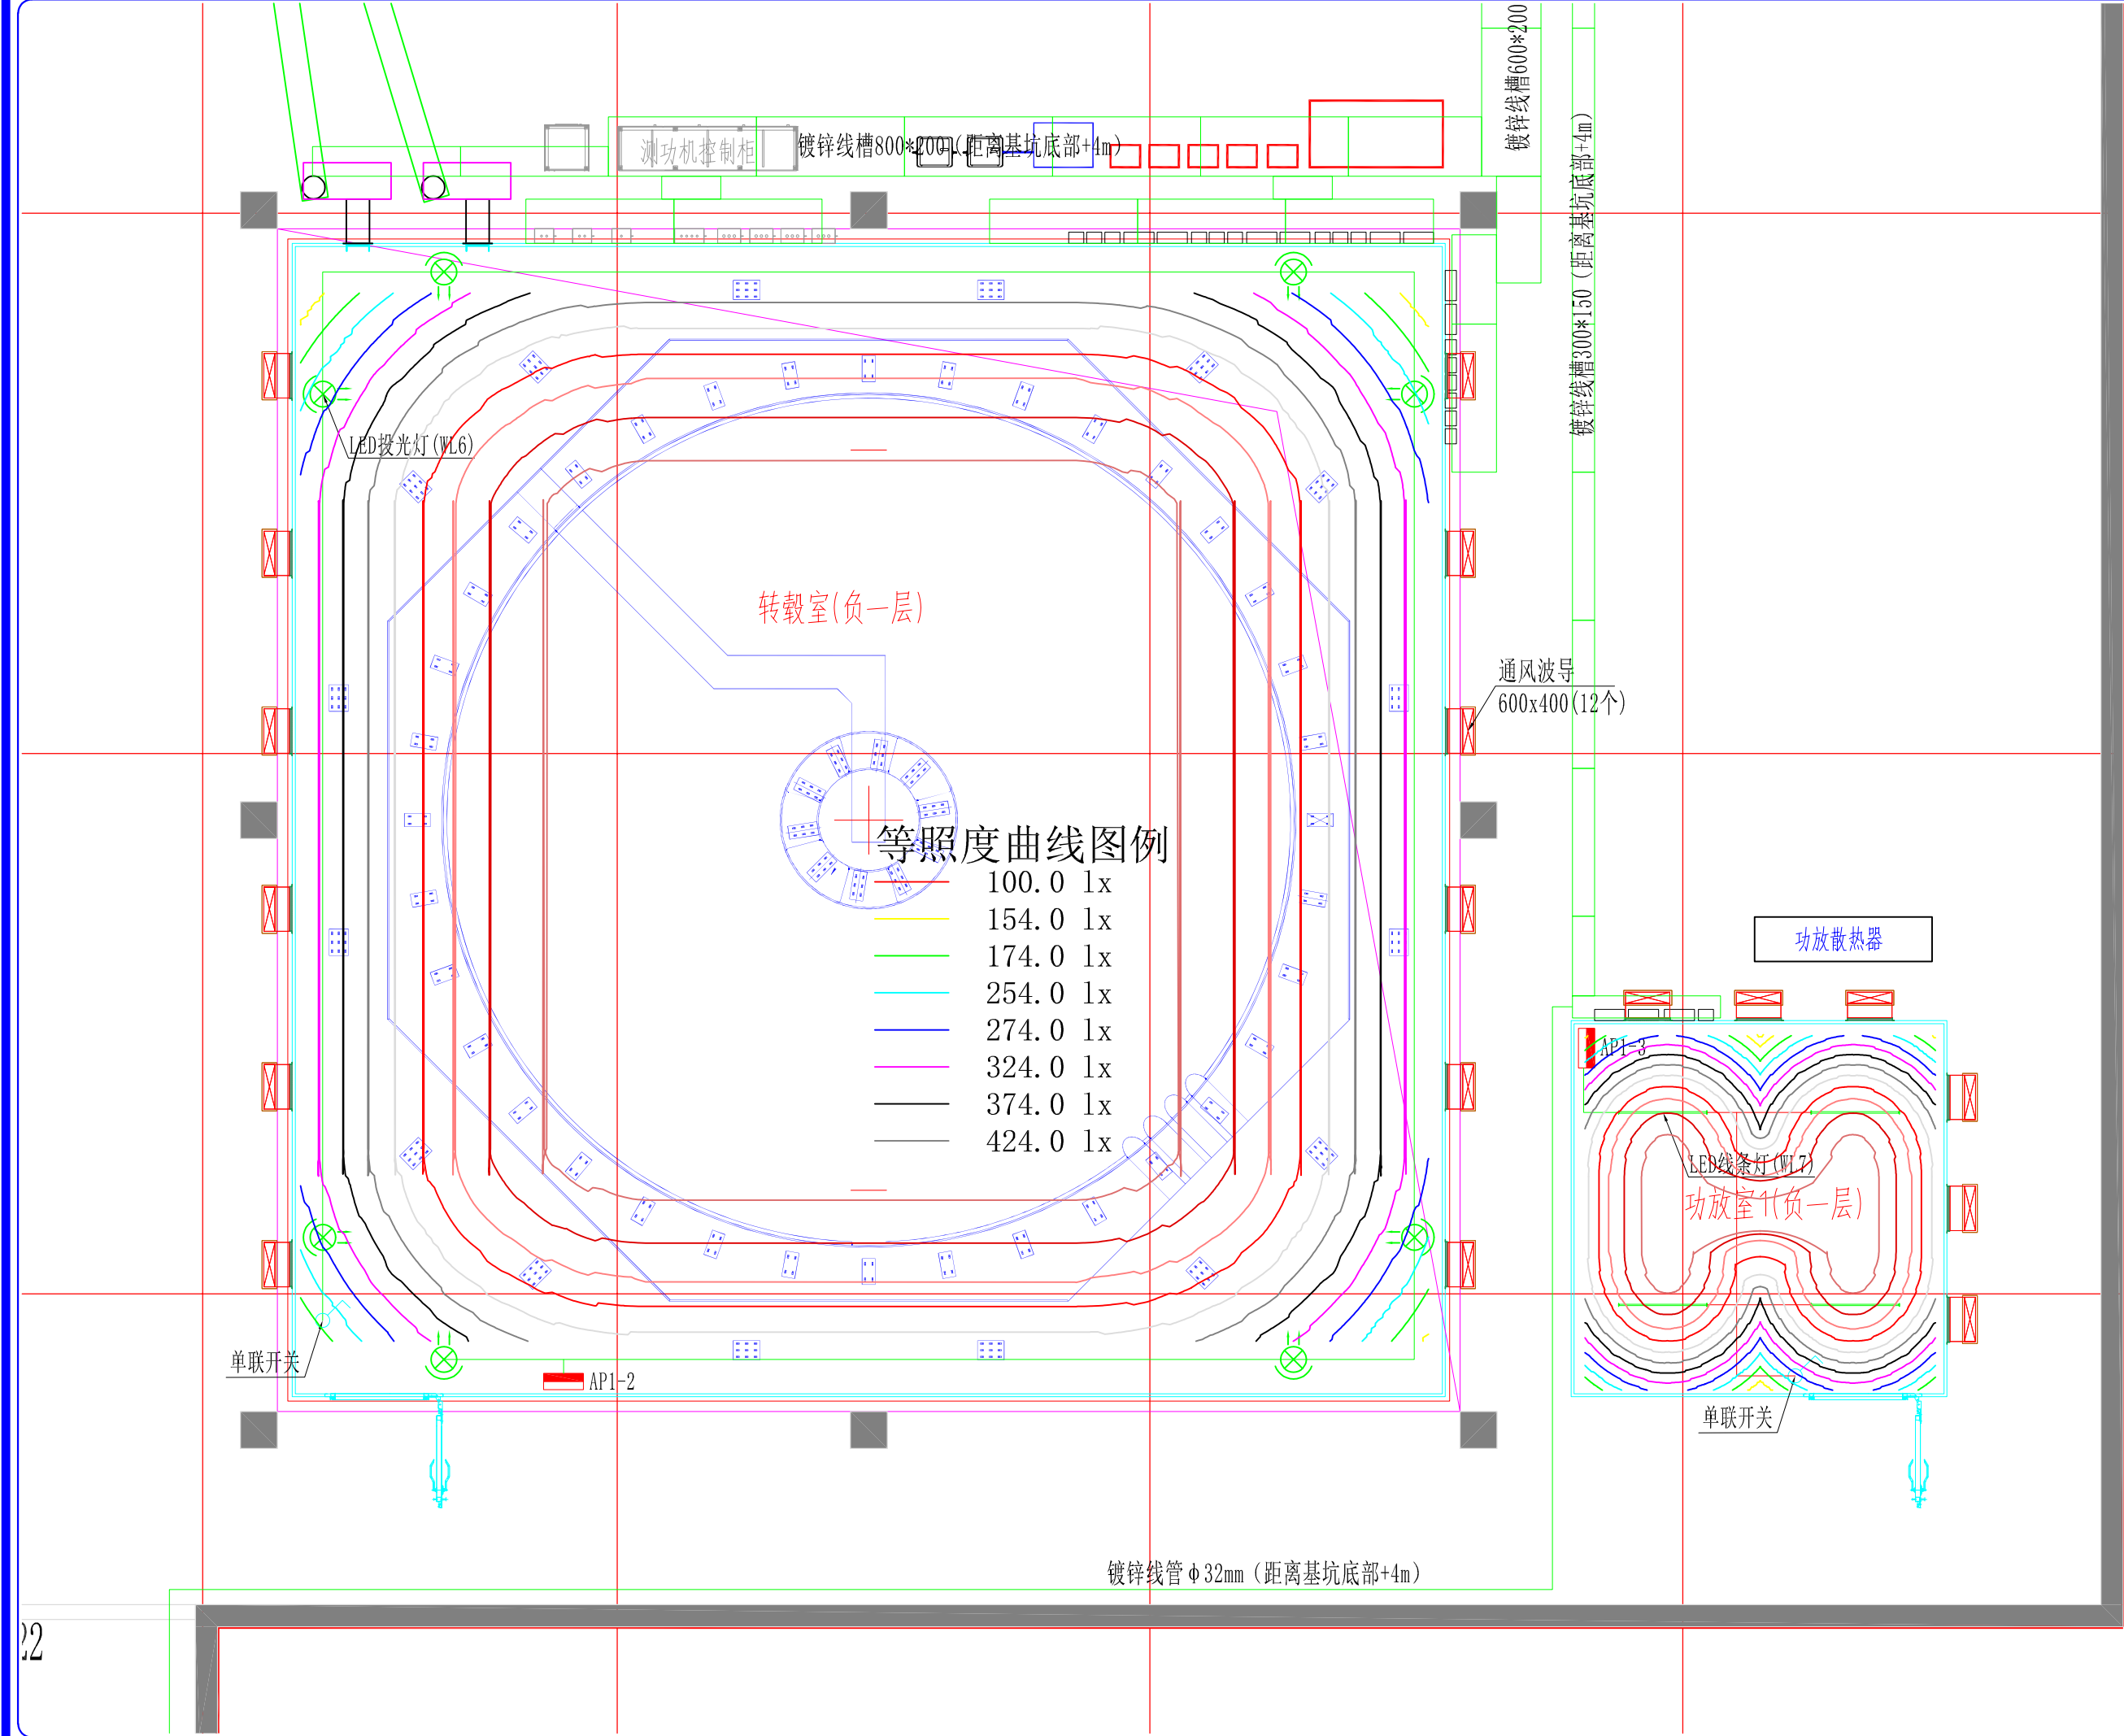

ETS·LINDGRENTM

An ESCO Technologies Company

Beijing Lindgren E.M. Technology Co., Ltd.

China Office :
No. 17 Madian East Road, Haidian Dist., Beijing, P.R.C
Beijing P.R.C100083
Tel: 8610-82730877 Fax: 8610-82730880

转载室&功放室照度布局图

This document and the information contained therein are the property of LINDGREN RF ENCLOSURES, INC. Glendide Heights, Illinois. Recipient agrees NOT to:

(1) Use such information for purposes other than those expressly authorized by LINDGREN RF ENCLOSURES, INC. without the express written permission of LINDGREN RF ENCLOSURES, INC. (2) Reproduce or copy this document in whole or in part without the express written permission of LINDGREN RF ENCLOSURES, INC.

REVISIONS DESCRIPTION	DATE	BY	REVISION

PROJECT TITLE:
NAST10m 转载室&OT A 转载室项目

CLIENT:

DESIGNED BY:
Zhang Haipeng

CHECKED BY:

MANAGER:

CUSTOMER:


DATE:
10-03-2025

SCALE:
NONE

方案

E

E5

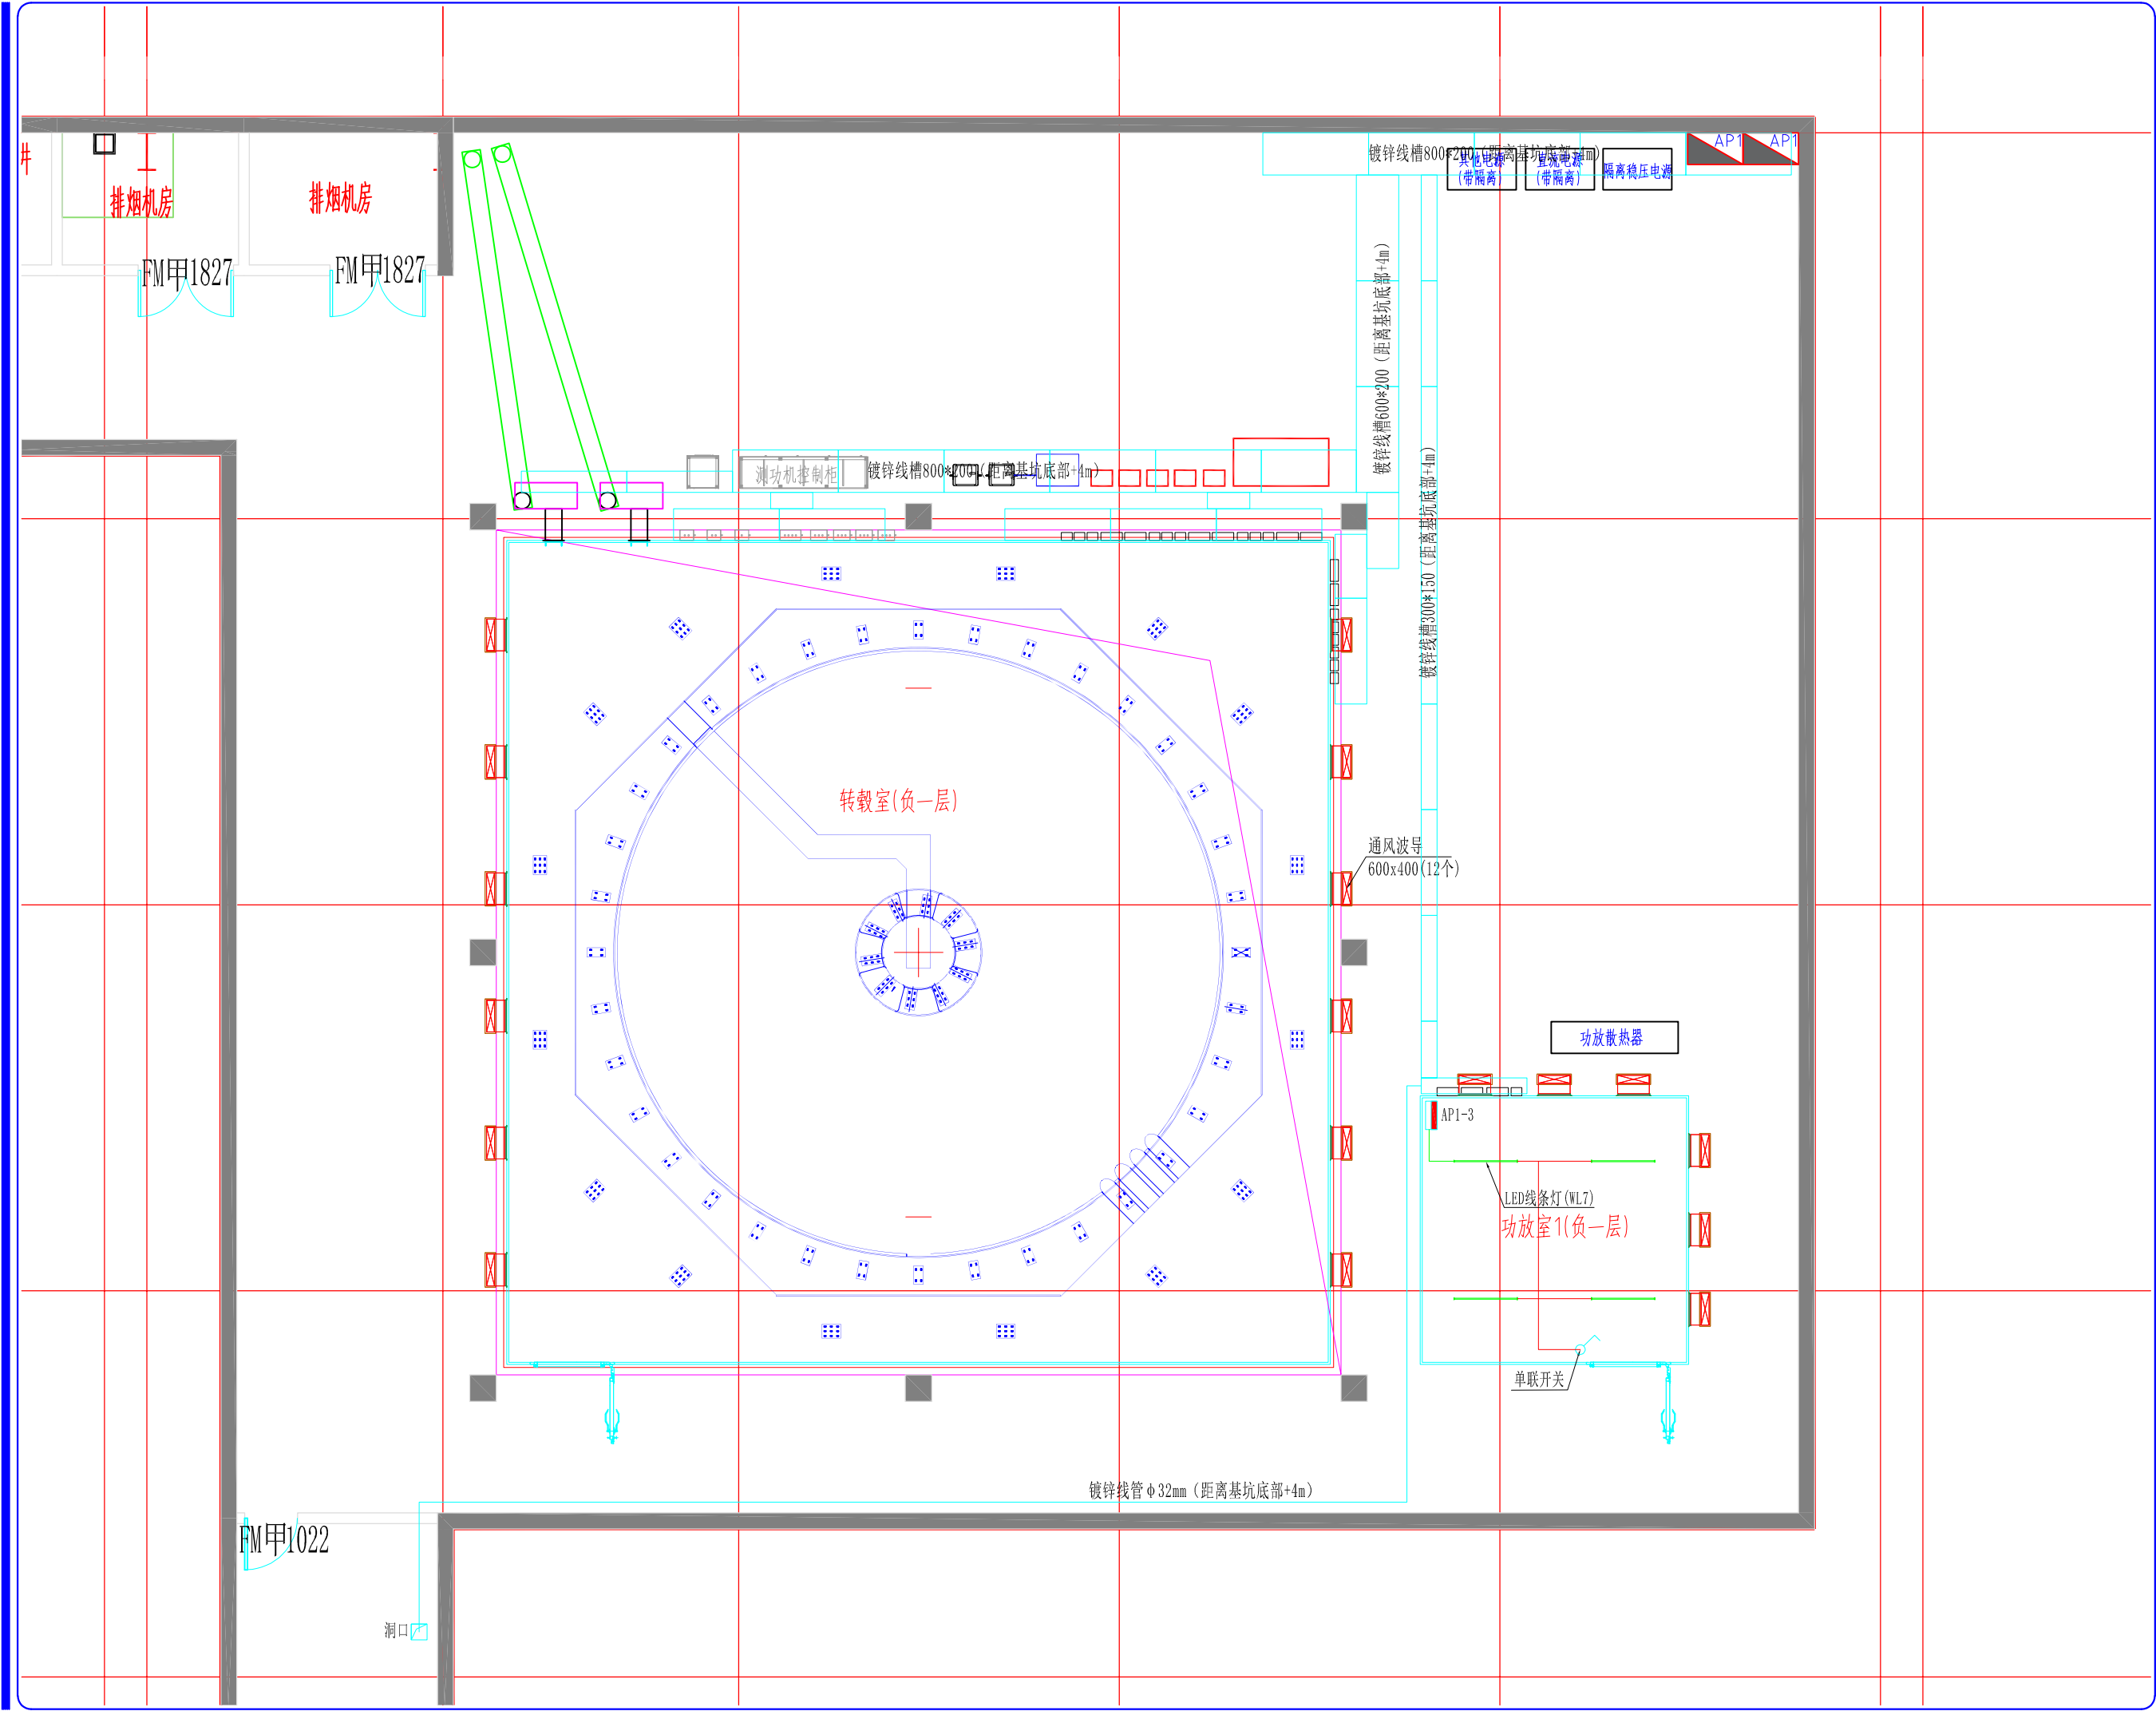



ETS LINDGREN

CHINA

An ESCO Technologies Company

Beijing Lindgren E.M. Technology Co., Ltd.

China Office :

No. 17 Madian East Road, Haidian Dist., Beijing, P.R.C

Beijing P.R.C100083

Tel: 8610-82730877 Fax: 8610-82730880

名称:

SHEET TITLE

室外线槽布局图

备注:

REVISIONS DESCRIPTION

此文档及其中包含的信息均为LINDGREN RF ENCLOSES, INC. 的财产。未经LINDGREN RF ENCLOSES, INC. 事先书面许可, 不得复制或传播。如有违反, 将追究其法律责任。

设计:

审核:

批准:

版本	描述	日期	设计	审核	批准

工程名称:

PROJECT TITLE

项目地址:

PROJECT ADDRESS

客户名称:

CUSTOMER NAME

客户地址:

CUSTOMER ADDRESS

客户电话:

CUSTOMER PHONE

客户传真:

CUSTOMER FAX

客户邮箱:

CUSTOMER EMAIL

客户网站:

CUSTOMER WEBSITE

客户备注:

CUSTOMER REMARKS

制图人:

DRAWN BY:

Zhang Haipeng

审核人:

CHECKED BY:

负责人:

MANAGER:

客户:

CUSTOMER:

日期:

DATE:

10-03-2025

比例:

SCALE:

NONE

工号:

JOB NO:

版本:

REV:

E

方案

图纸编号:

DRAWING NO:

E6