


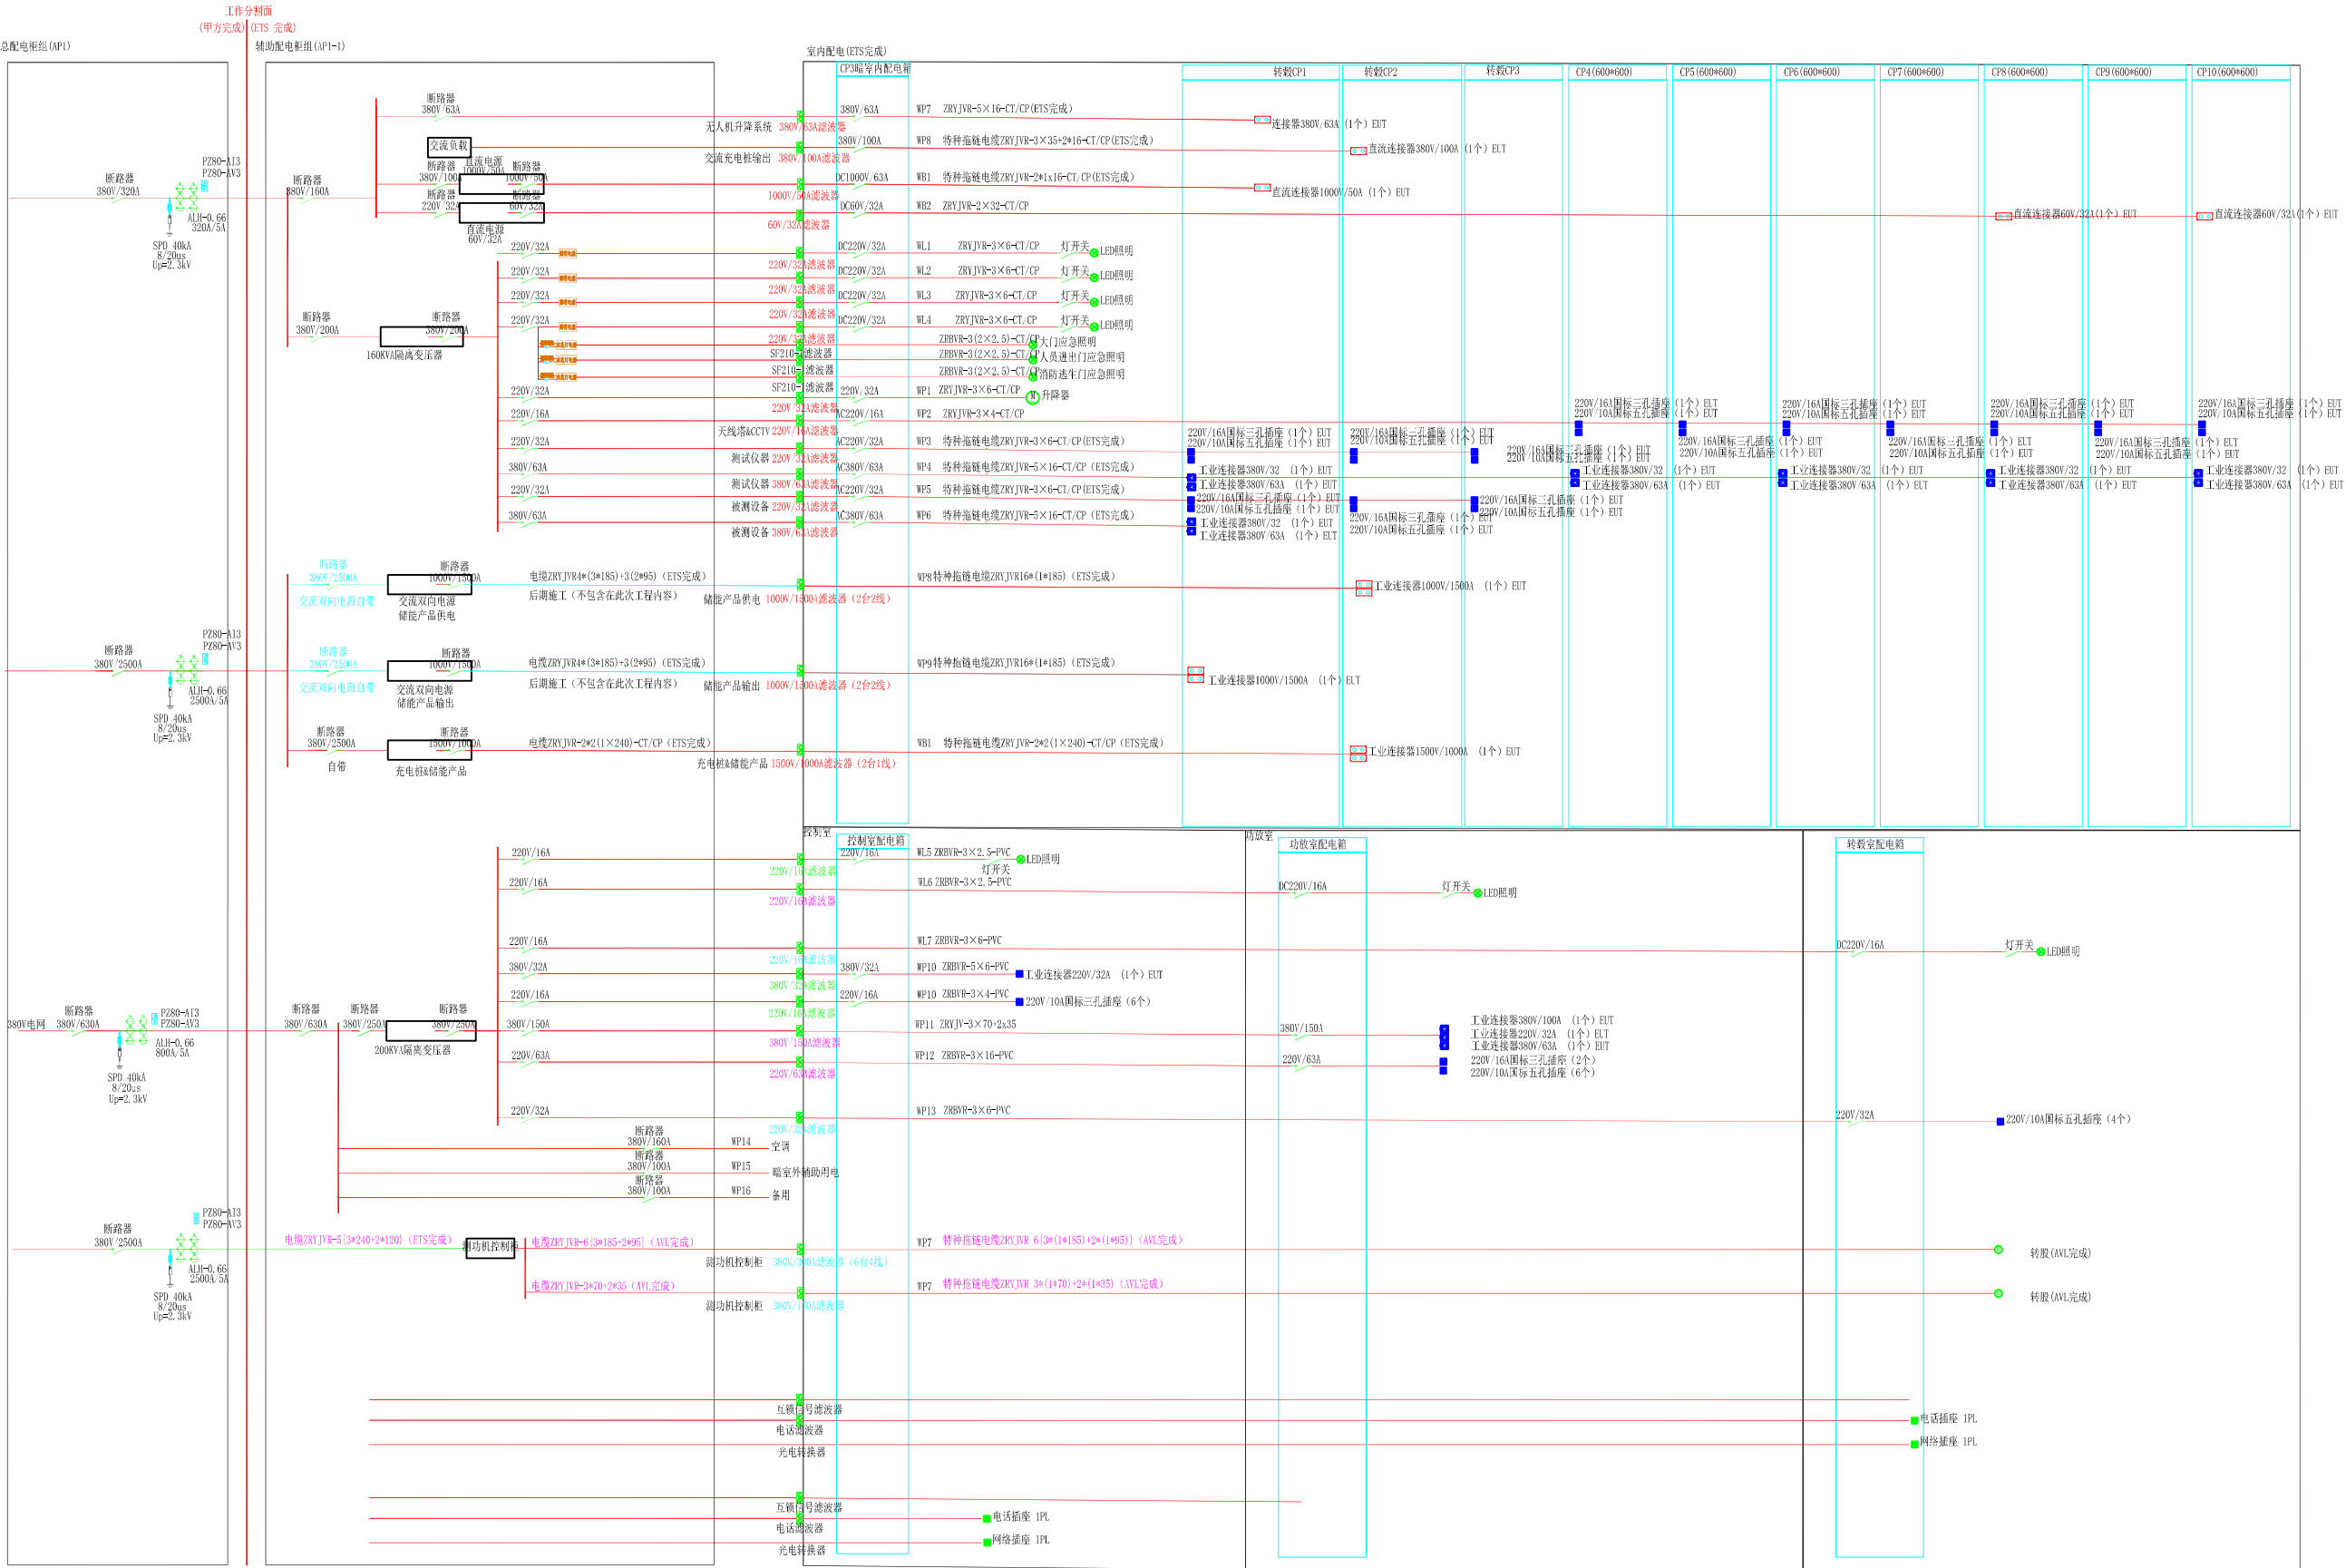

整车场响室配电系统图

版本: SHEET TITLE

版本: SHEET TITLE

工程名称: PROJECT TITLE
地址: ADDRESS
NAS10m峰室&01A峰室项目

制图人: DRAWN BY: Zhang Haipeng
审核人: CHECKED BY:
负责人: MANAGER:
客户: CUSTOMER:
日期: DATE: 10-28-2025
比例: SCALE: NONE

方案 E

图纸编号: DRAWING NO:
E1



ETS·LINDGRENTM

An ESCO Technologies Company

Beijing Lindgren E.M. Technology Co., Ltd.

China Office :
No. 17 Madian East Road, Haidian Dist., Beijing, P.R.C
Beijing P.R.C100083
Tel:8610-82730877 Fax:8610-82730880

整车场响室内配电系统图

姓名: SHEET TITLE

REVISIONS DESCRIPTION

版本: 描述

工程名称: PROJECT TITLE

地址: ADDRESS

客户: CUSTOMER


制图人: Zhang Haipeng


审核人: 审核人: MANAGER

日期: 10-28-2025 比例: NONE

方案 E

E1.2

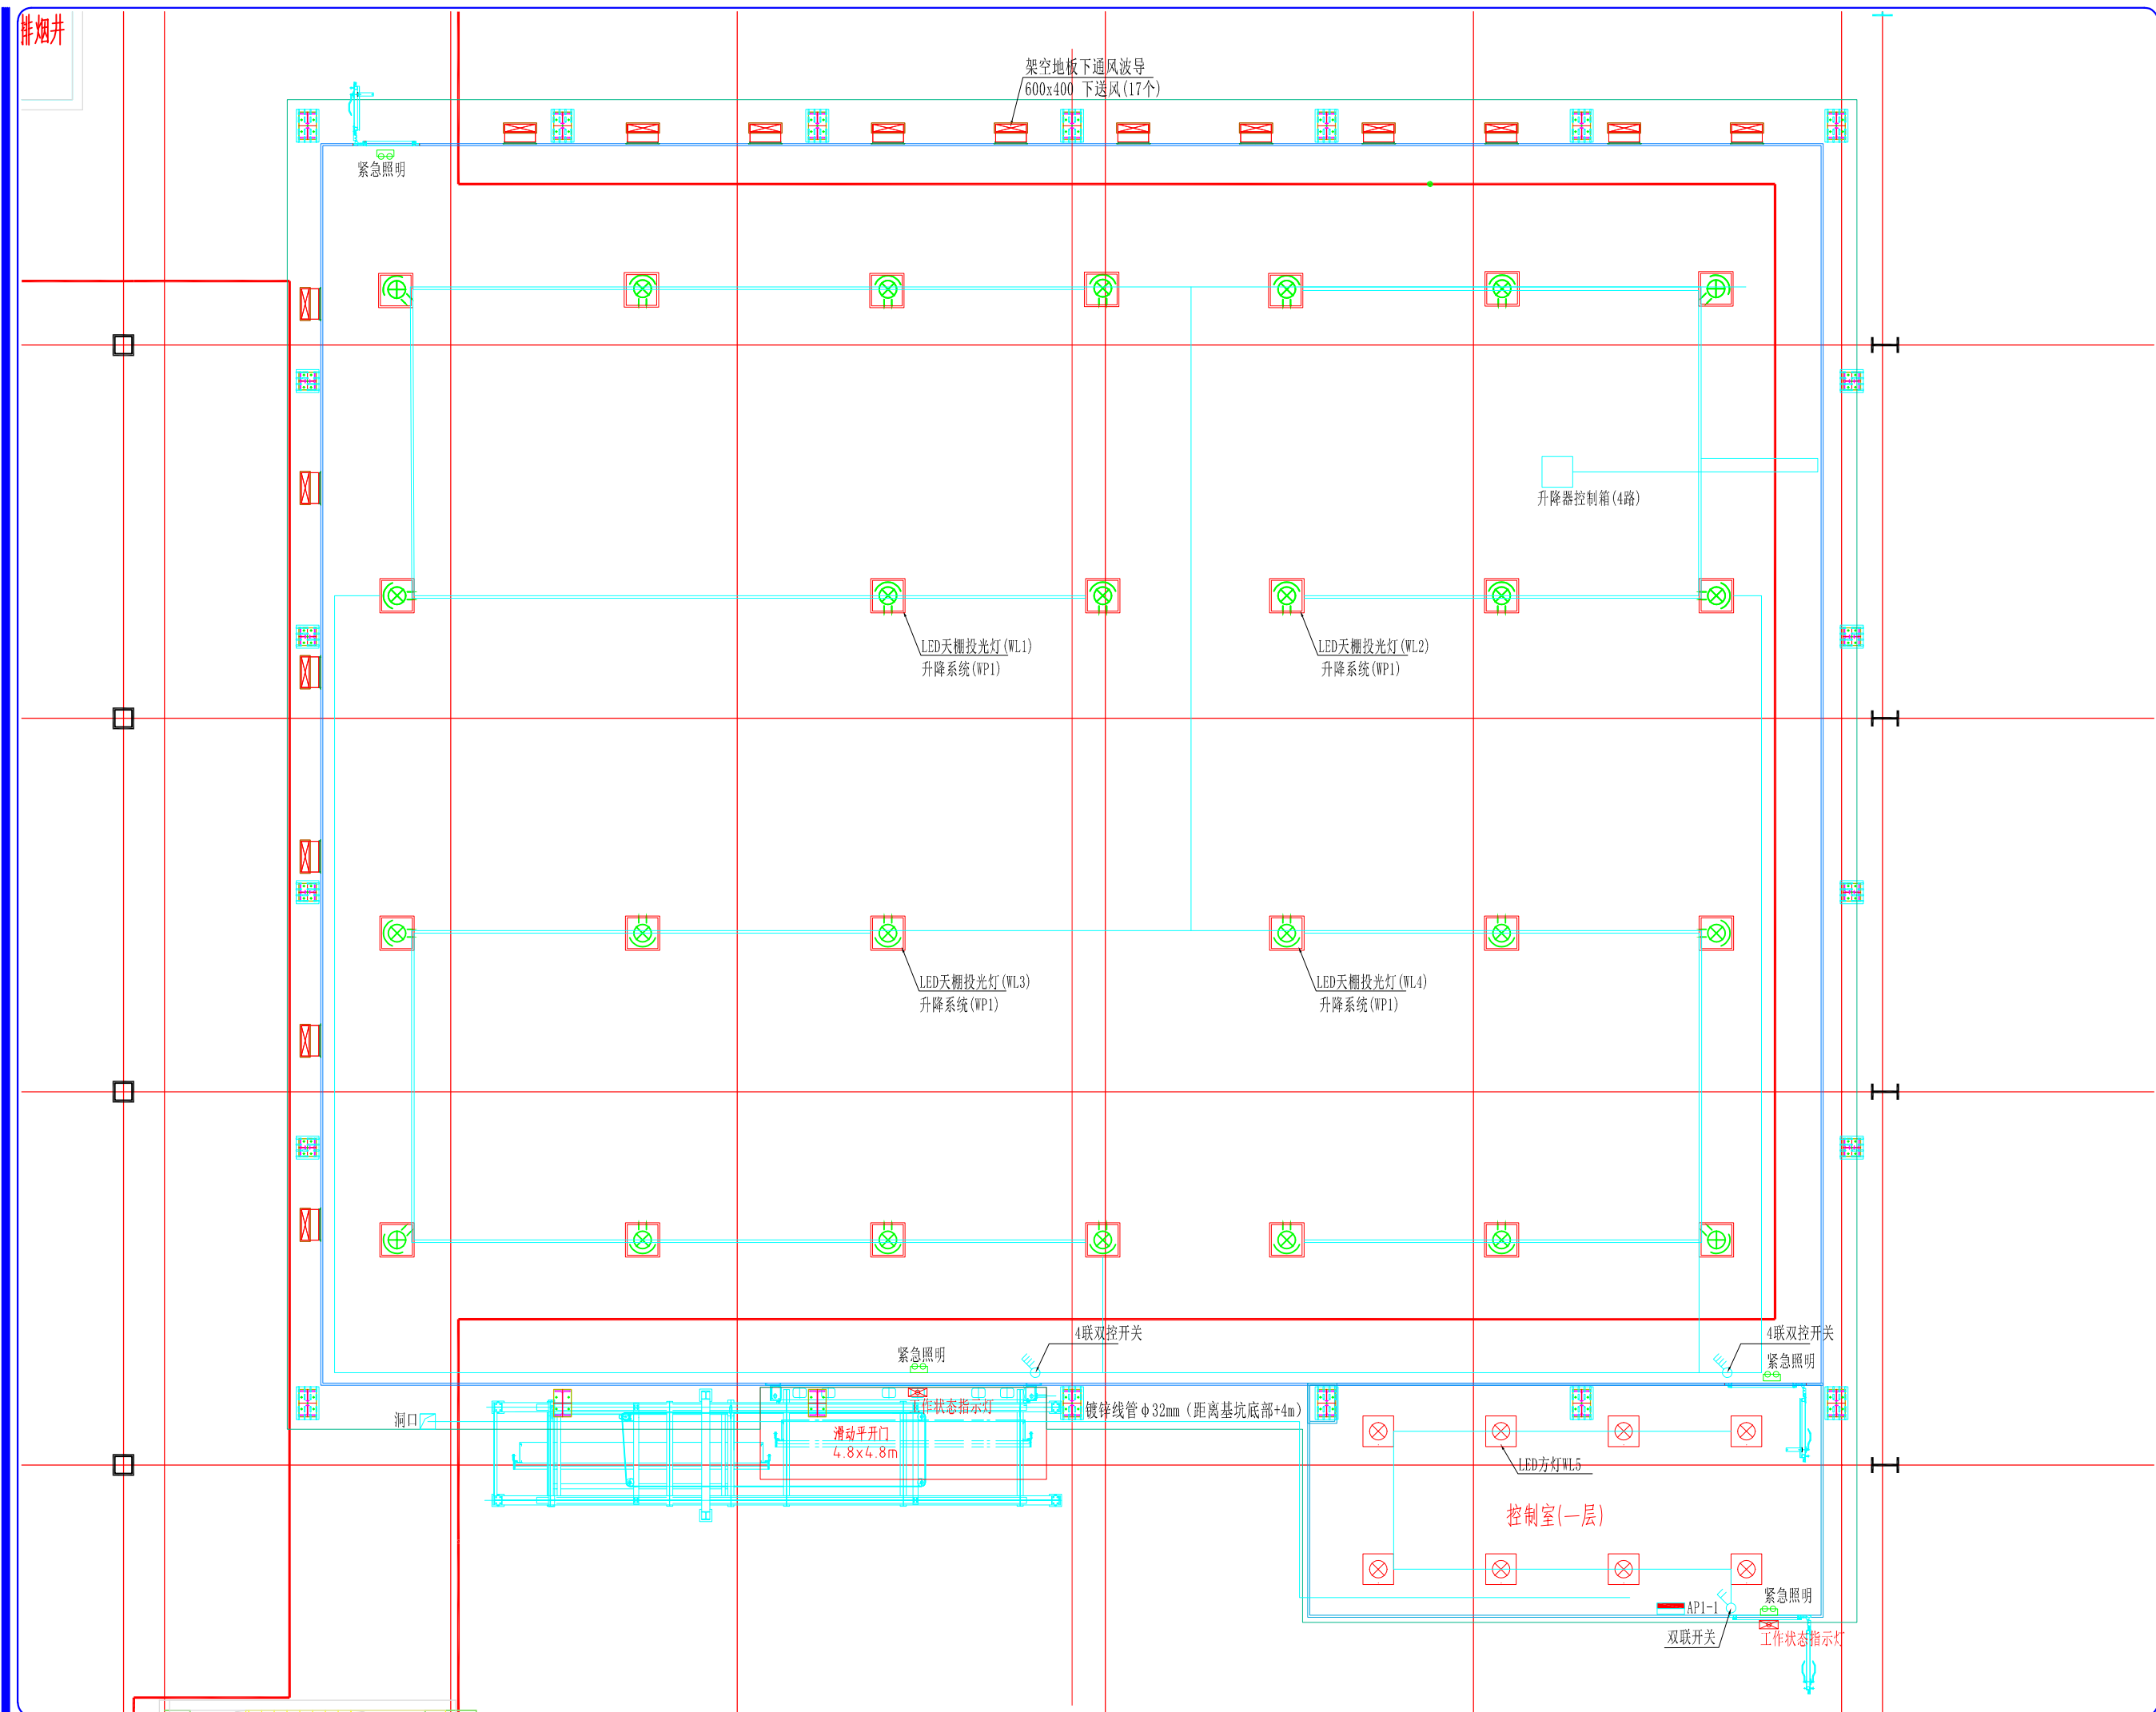

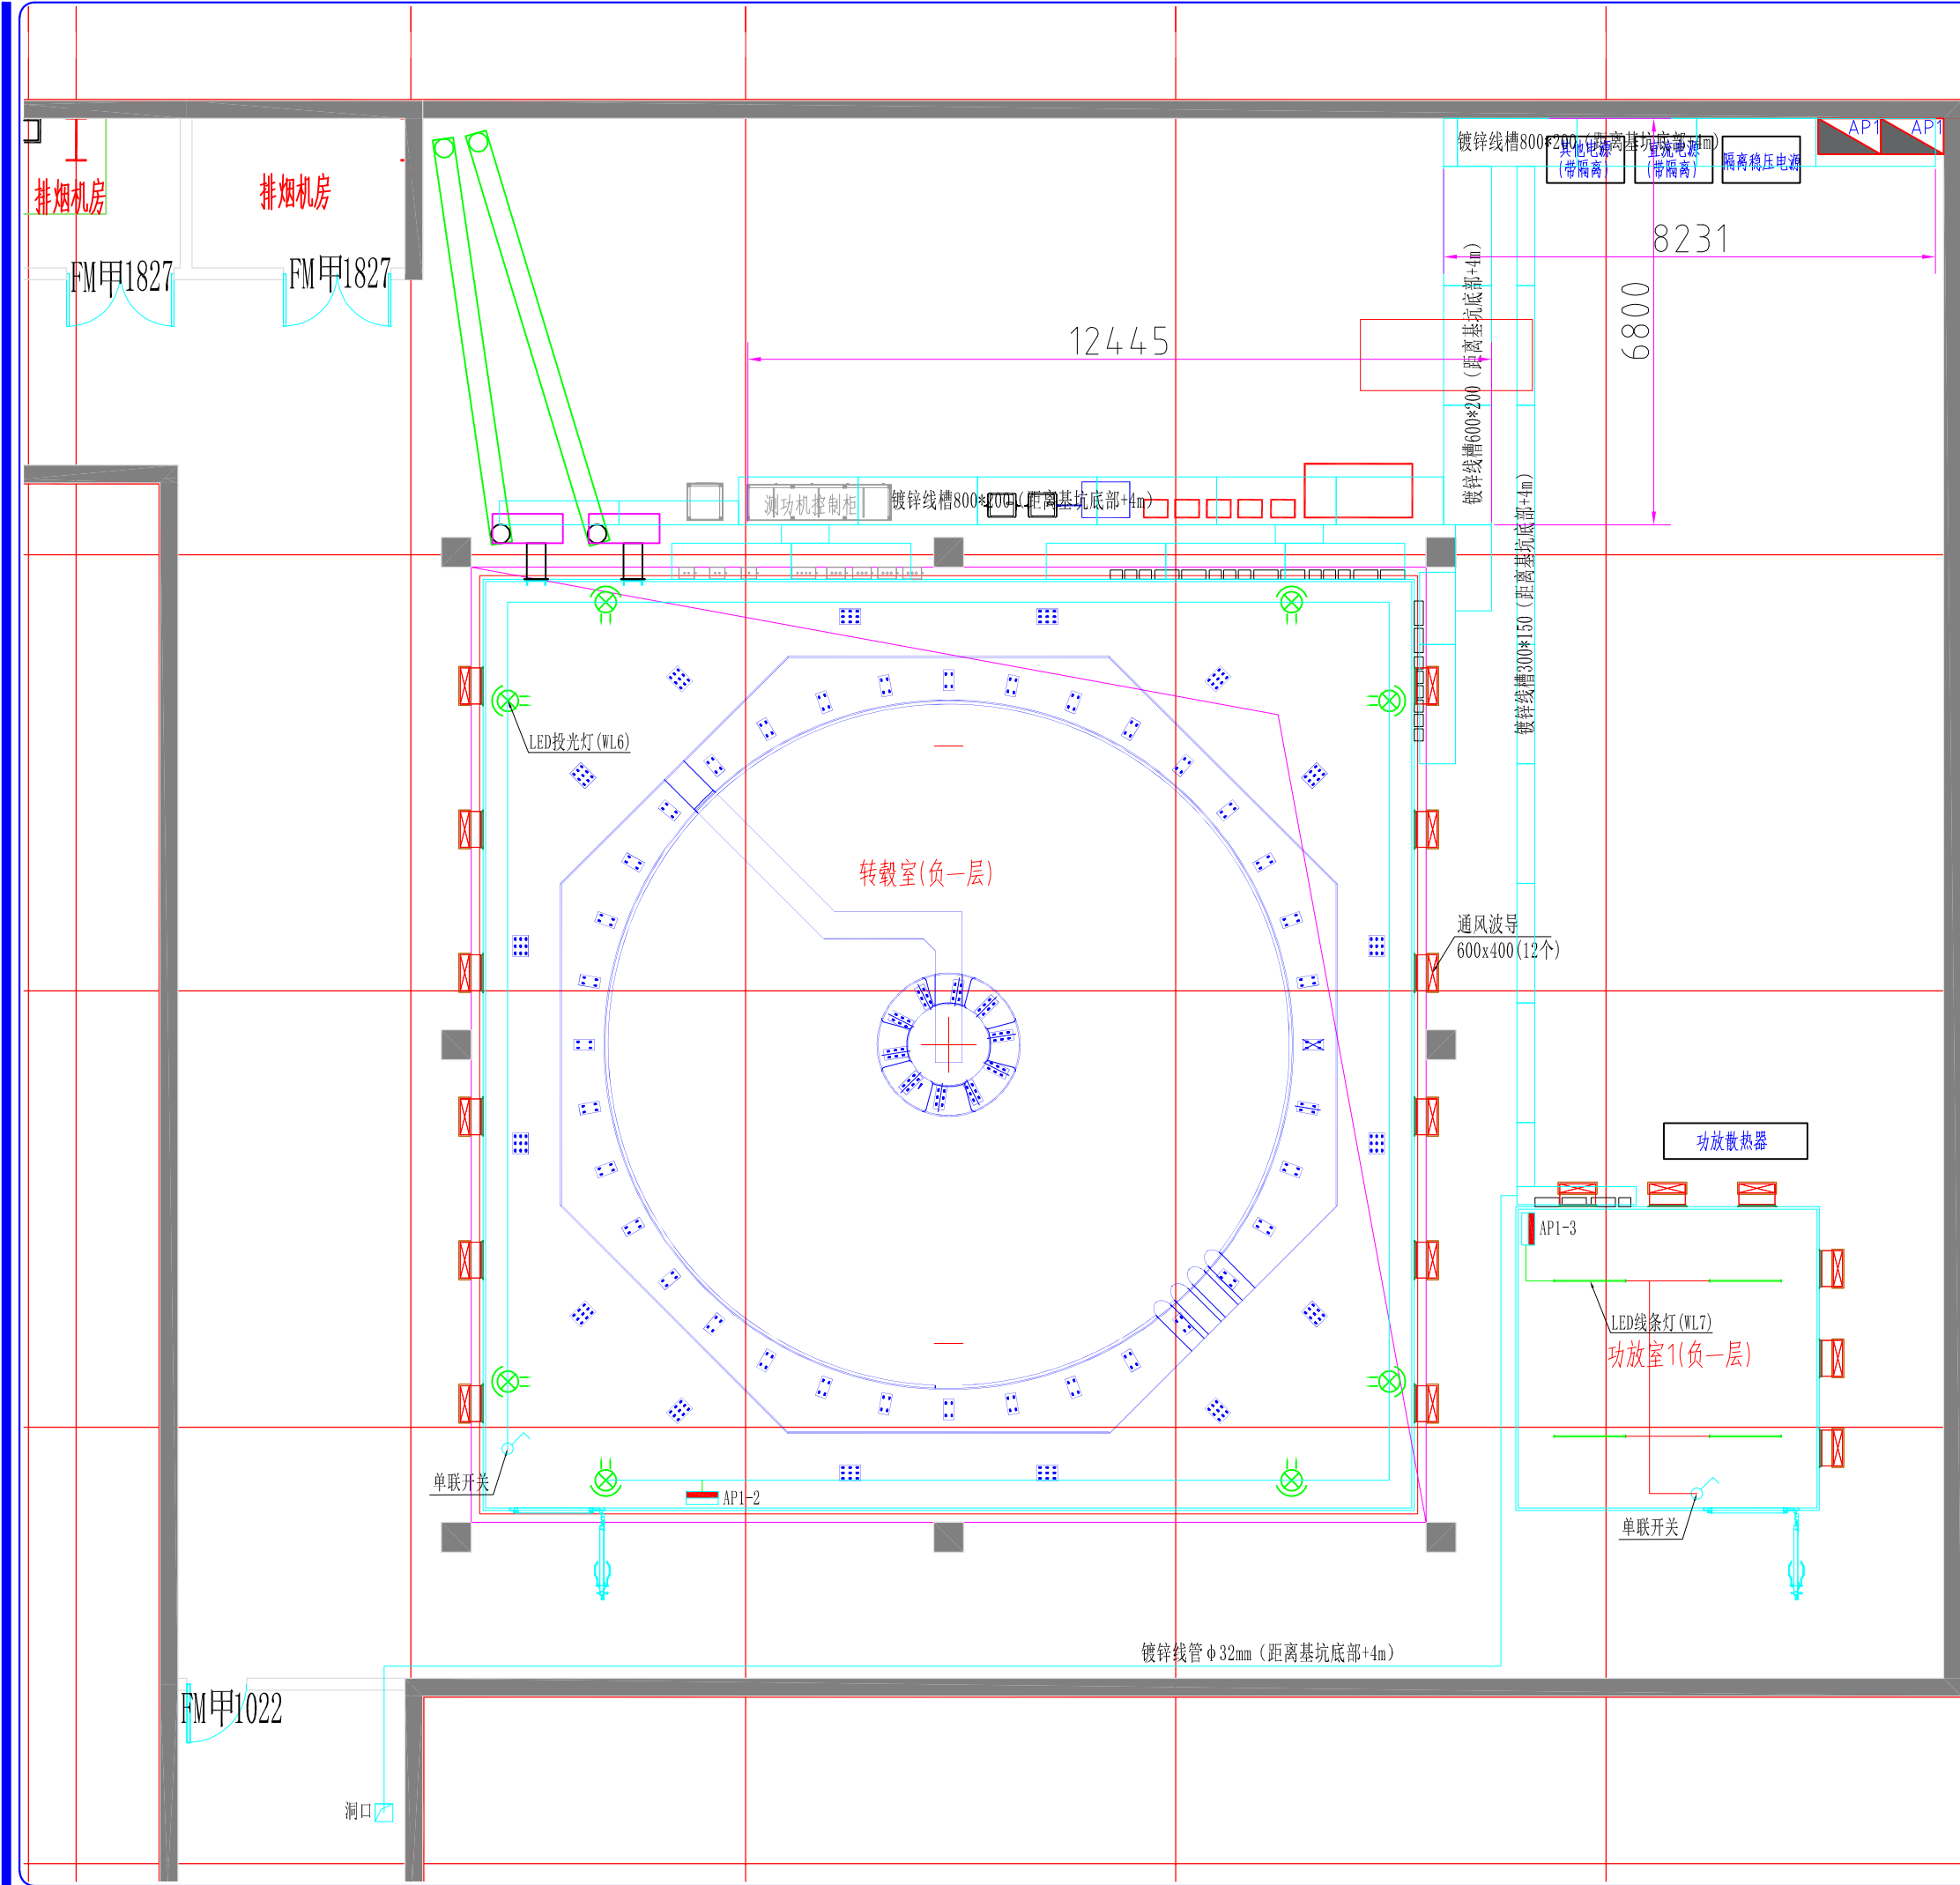

ETS·LINDGRENTM

An ESCO Technologies Company

Beijing Lindgren E.M. Technology Co., Ltd.

China Office :
No. 17 Madian East Road, Haidian Dist., Beijing, P.R.C
Beijing P.R.C100083
Tel: 8610-82730877 Fax: 8610-82730880

转裁室 & 功放室照明布局图

This document and the information contained therein are the property of LINDGREN RF ENCLOSURES, INC. Glendale Heights, Illinois. Recipient agrees NOT to:

(1) Use such information for purposes other than those expressly authorized by LINDGREN RF ENCLOSURES, INC. without the express written permission of LINDGREN RF ENCLOSURES, INC. (2) Reproduce or copy this document either in whole or in part without the express written permission of LINDGREN RF ENCLOSURES, INC.

REVISIONS DESCRIPTION	DATE	BY	DESCRIPTION

PROJECT TITLE: NAST 10m 转裁室 & 0.1A 功放室项目

ADDRESS:

Drawn by: Zhang Haipeng

Checked by:

Manager:


Customer:

Date: 10-28-2025 Scale: NONE

Job No: 方案

Rev: E

Drawing No: E3

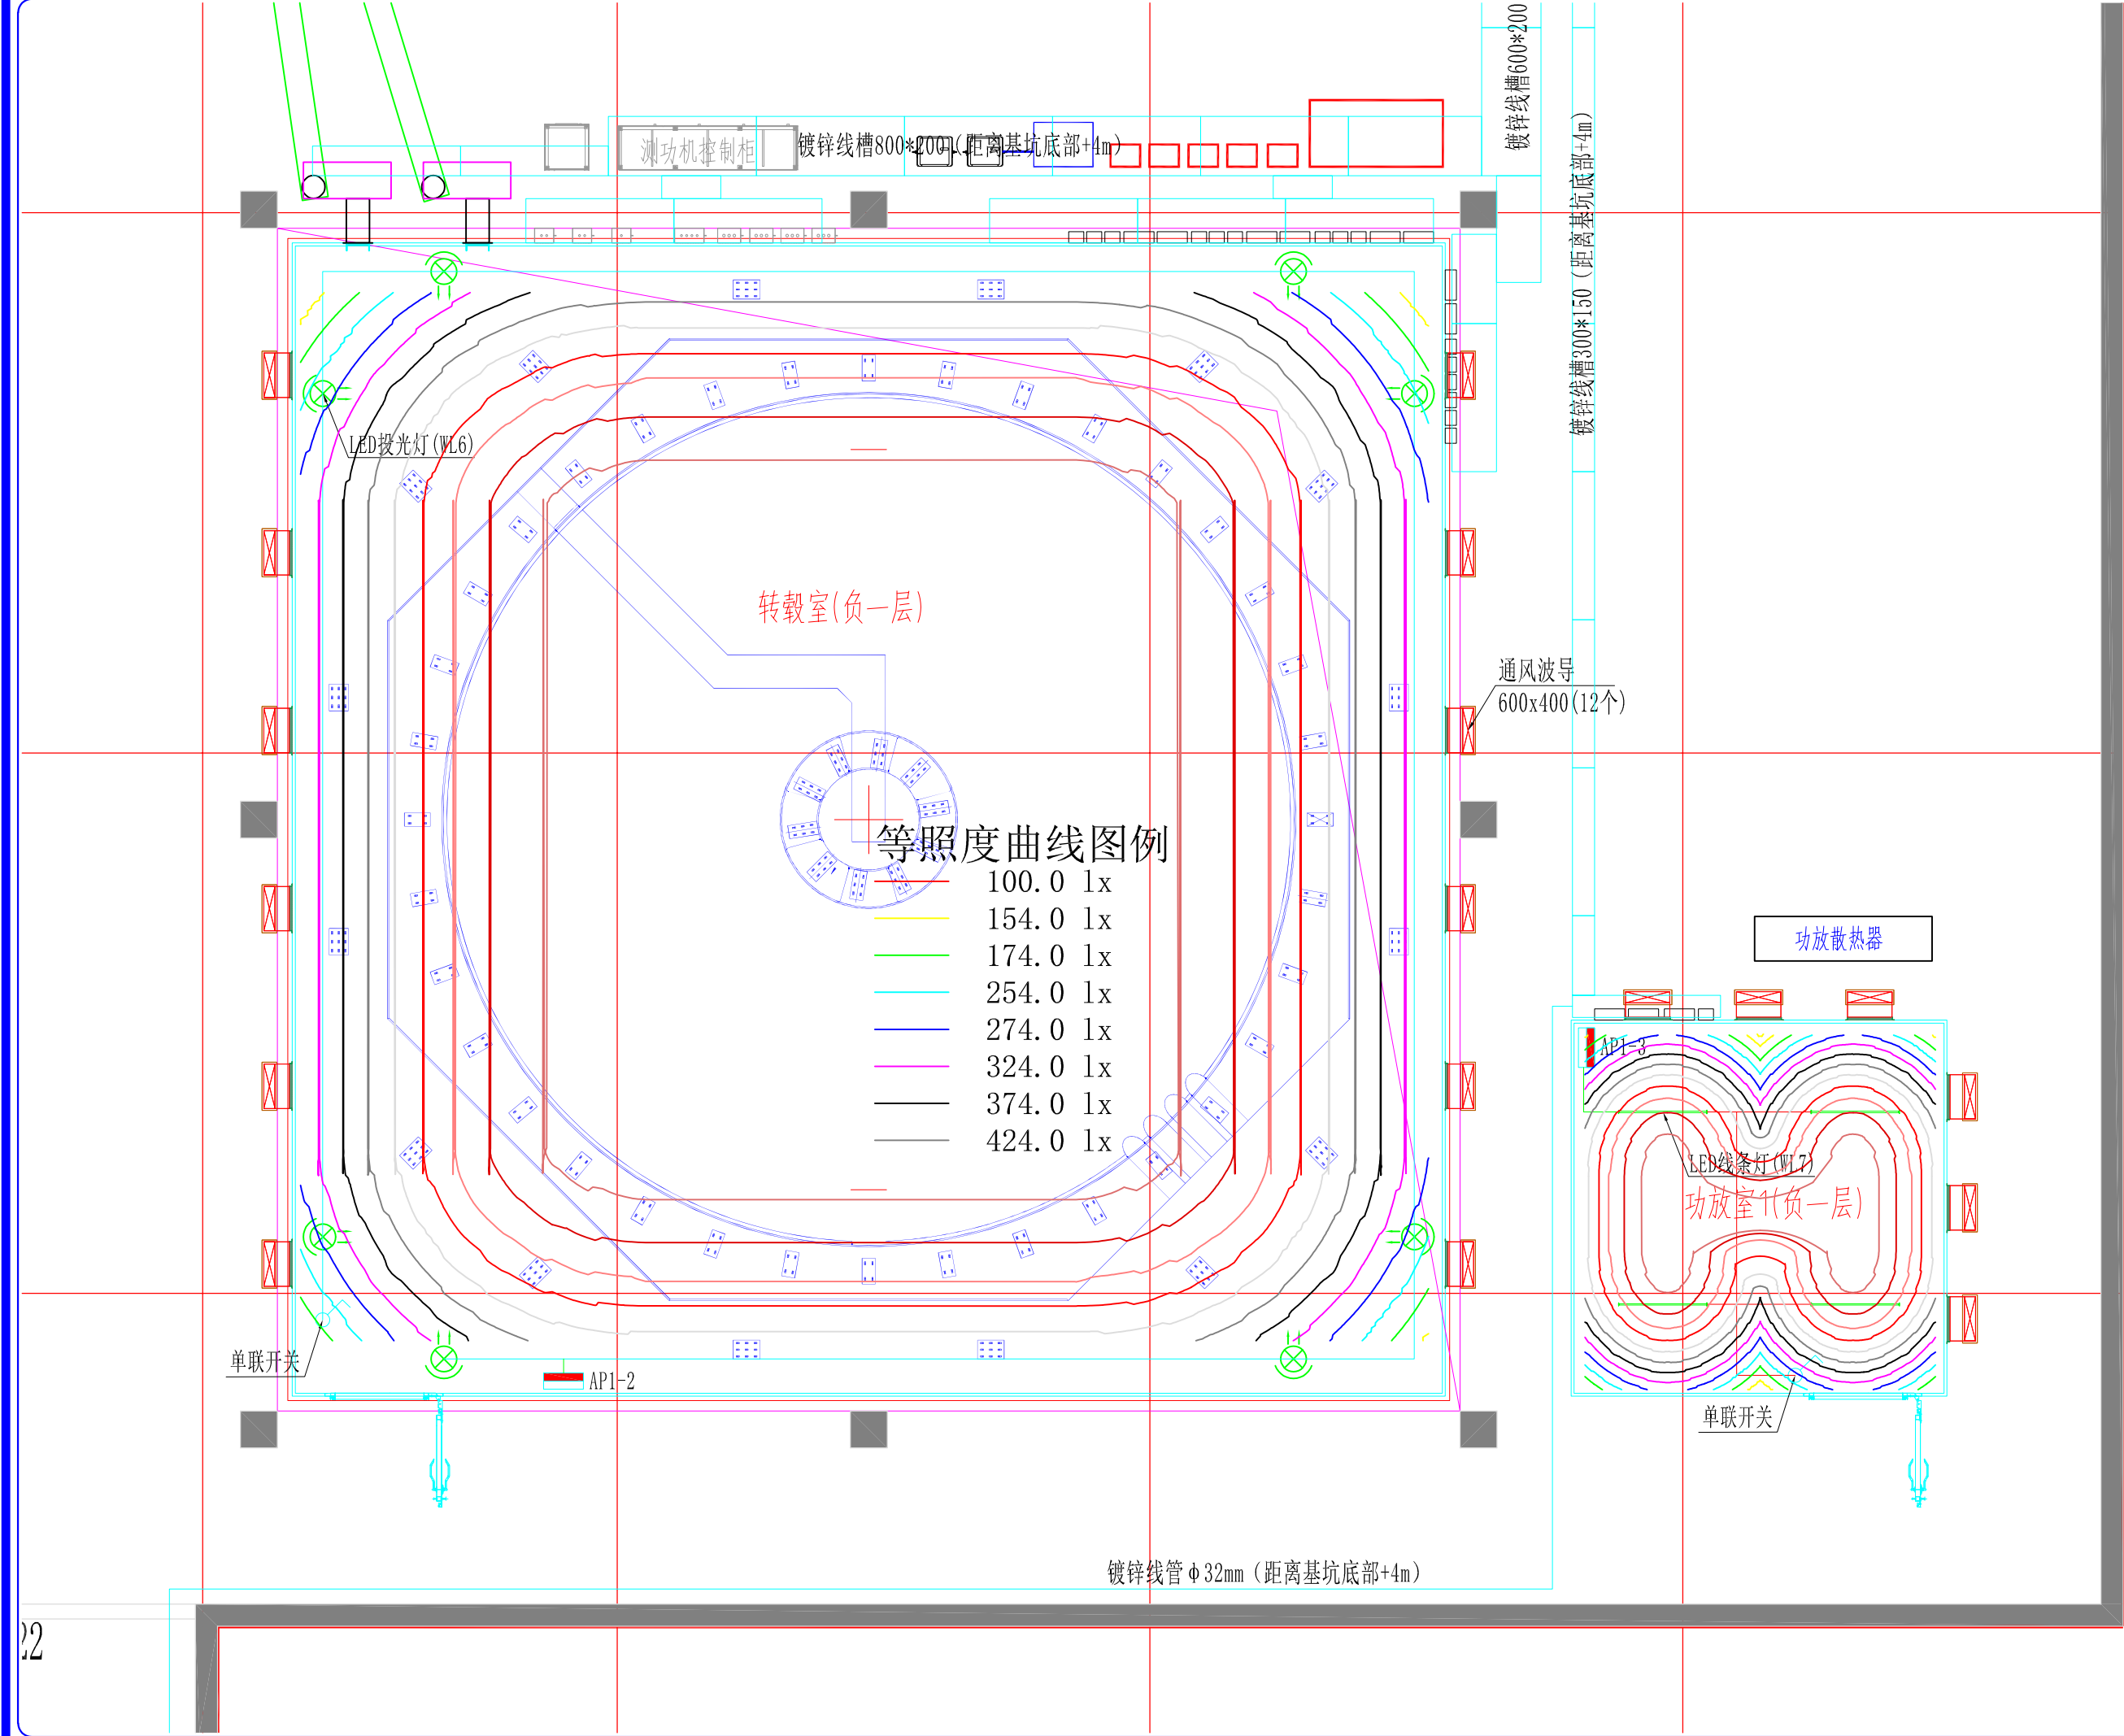

等照度曲线图例

- 100.0 lx
- 154.0 lx
- 174.0 lx
- 254.0 lx
- 274.0 lx
- 324.0 lx
- 374.0 lx
- 424.0 lx

