
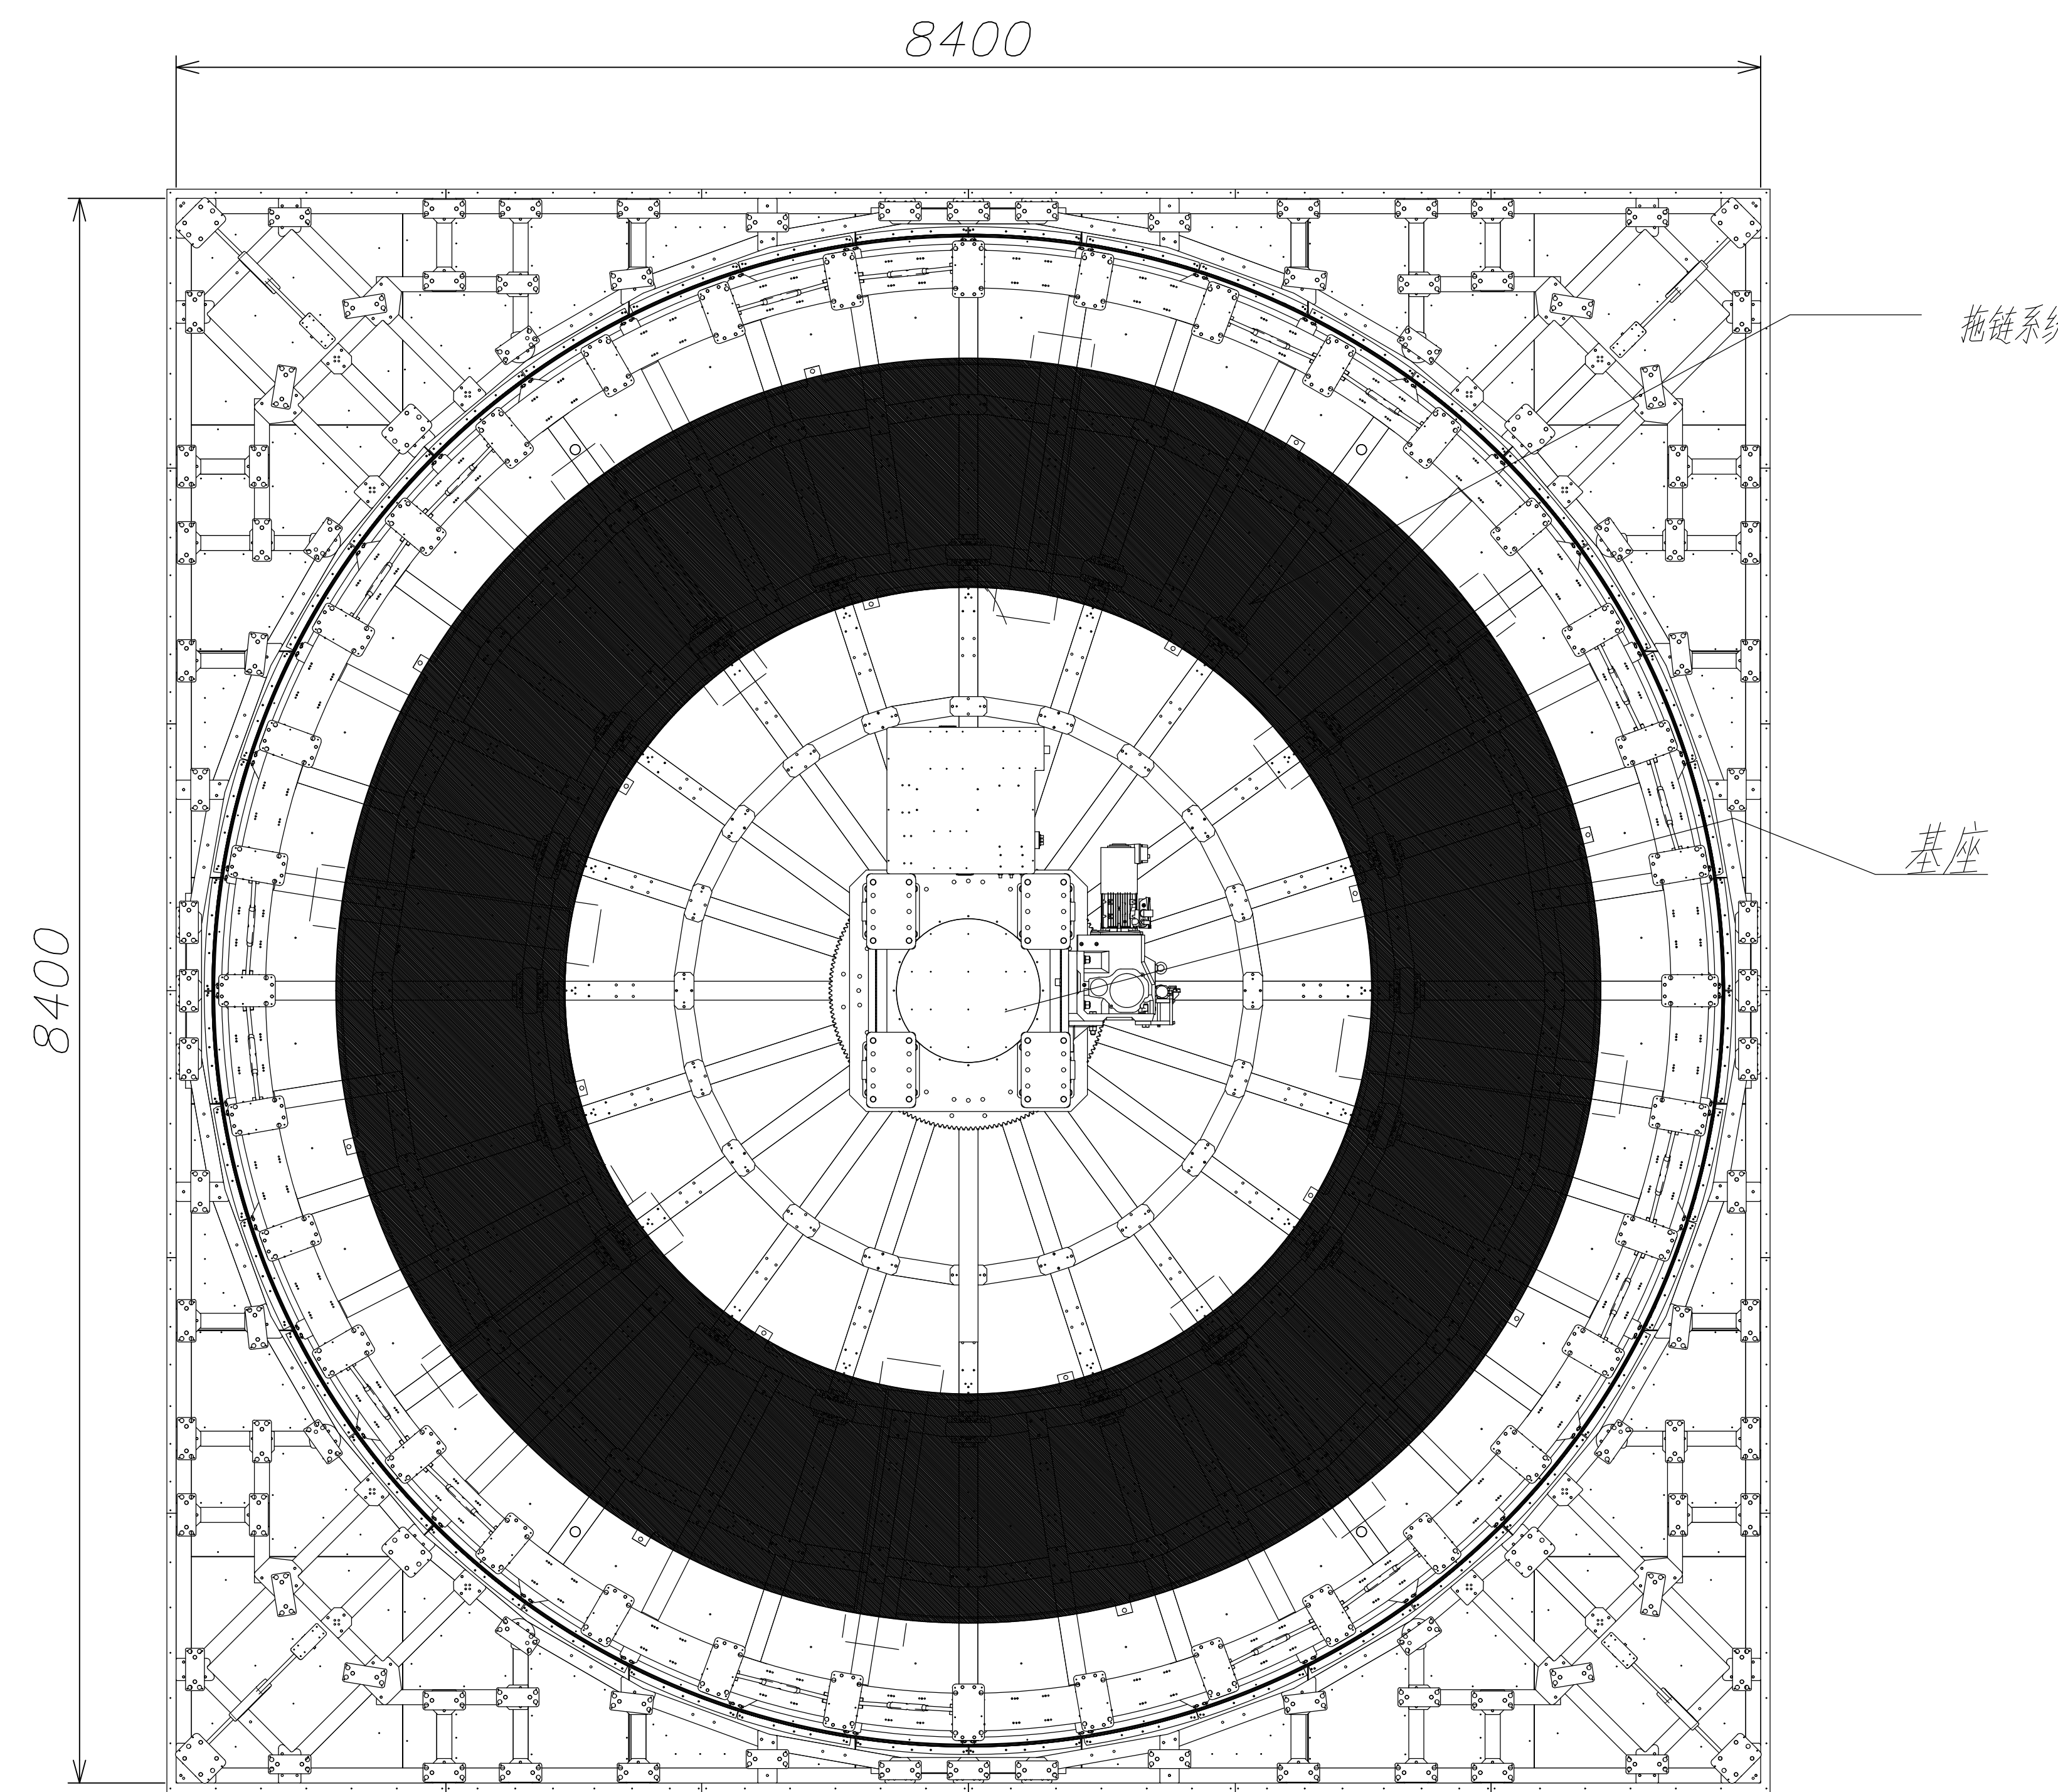
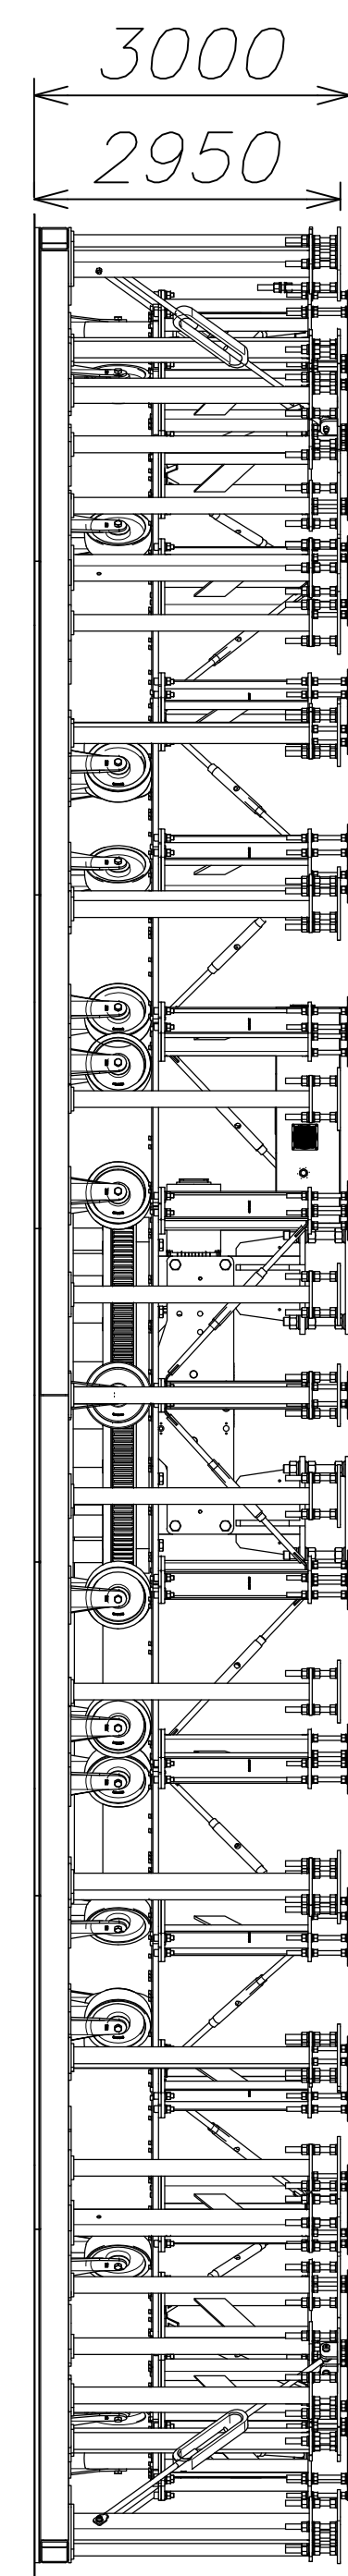


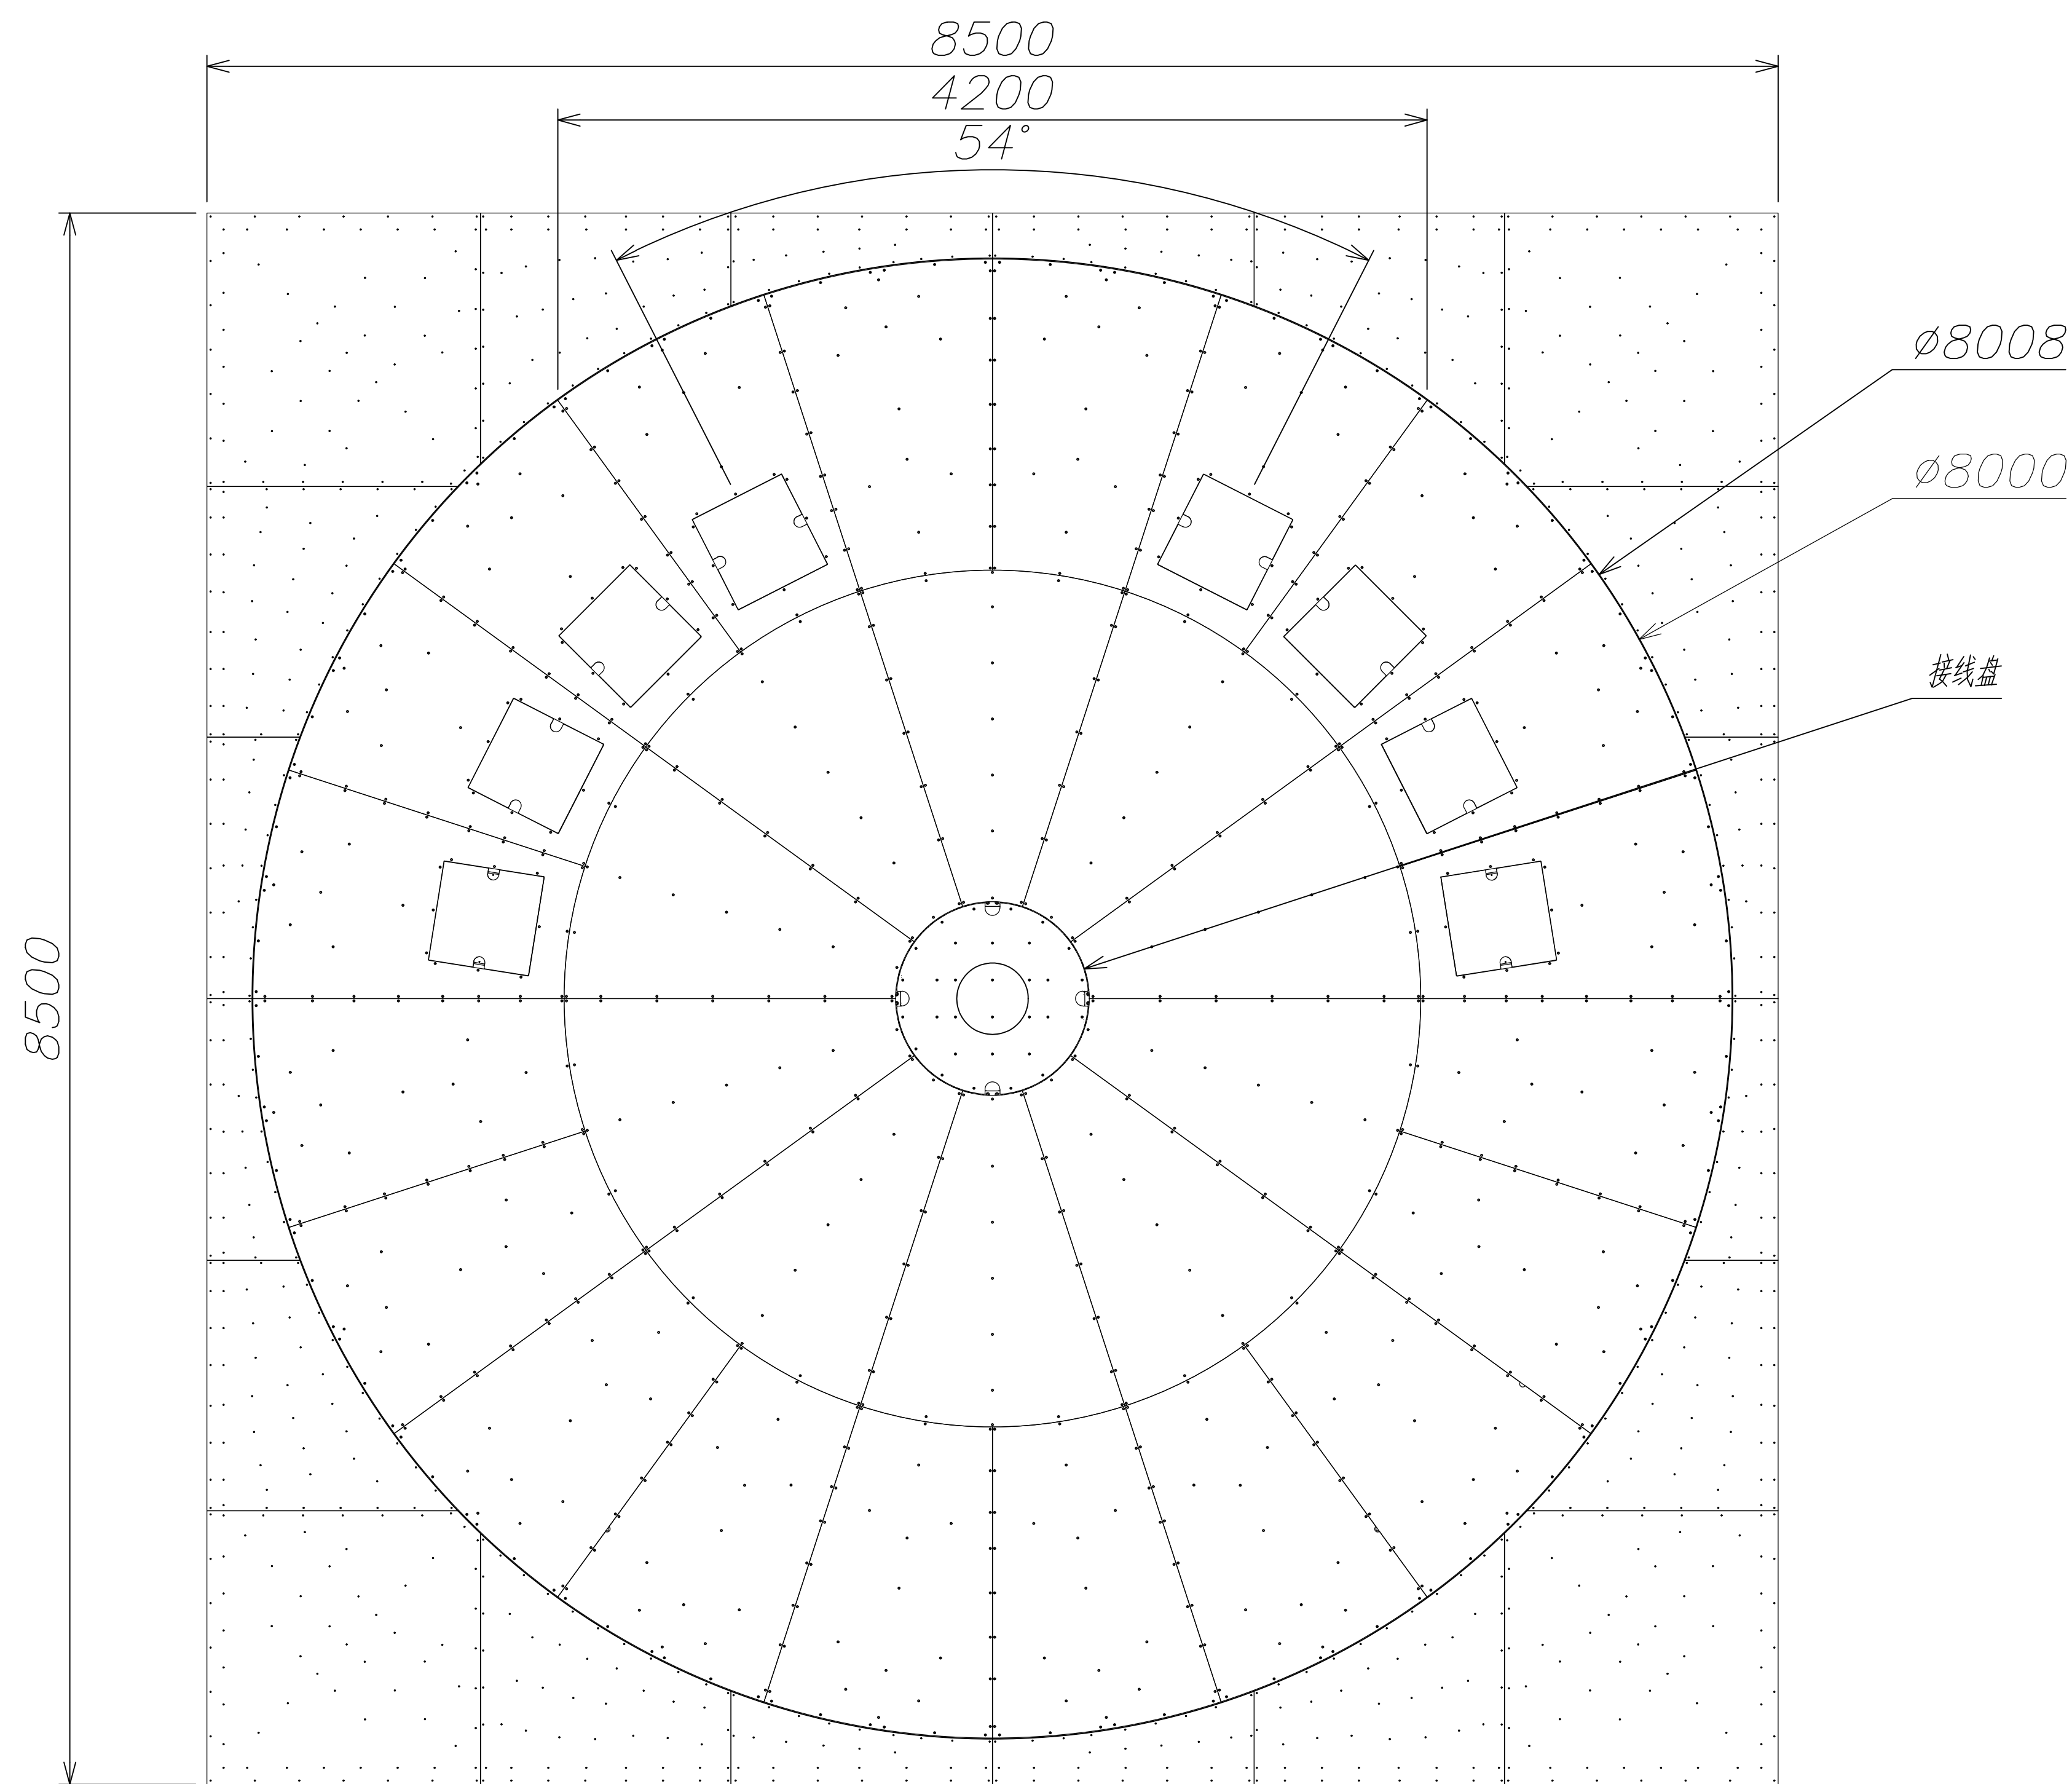

8米转台（内置回转拖链系统）投影

1. 圆盘直径8米，使用5mm不锈钢板+加强筋板，四周方盖板使用3mm不锈钢盖板；

圆盖板与方盖板之间的缝隙为4mm；

2. 外框8.5米（与反射地板搭接），内框8.4米；

4. 转台底座托底安装，四周框架、轨道垫平；

5. 转台高度3000mm，


1、定制单线滤波器，2000A，1500VAC 50/60Hz，16条中压柔性电缆，16个高压插头插座；

2、定制单线滤波器，1600A 3000V（4个并联满足6,000A），用于三相四线 6000A，3000V，80条中压柔性电缆，80条铜排转接；

3、拖链1接地线，一条，一条单芯柔性电缆，1个高压插头插座；


4、拖链2接地线，一条，一条单芯柔性电缆，1个高压插头插座；

5、定制单线滤波器，1400A1500V（6个并联满足7.000A），用于直流二线 7000A 1500V

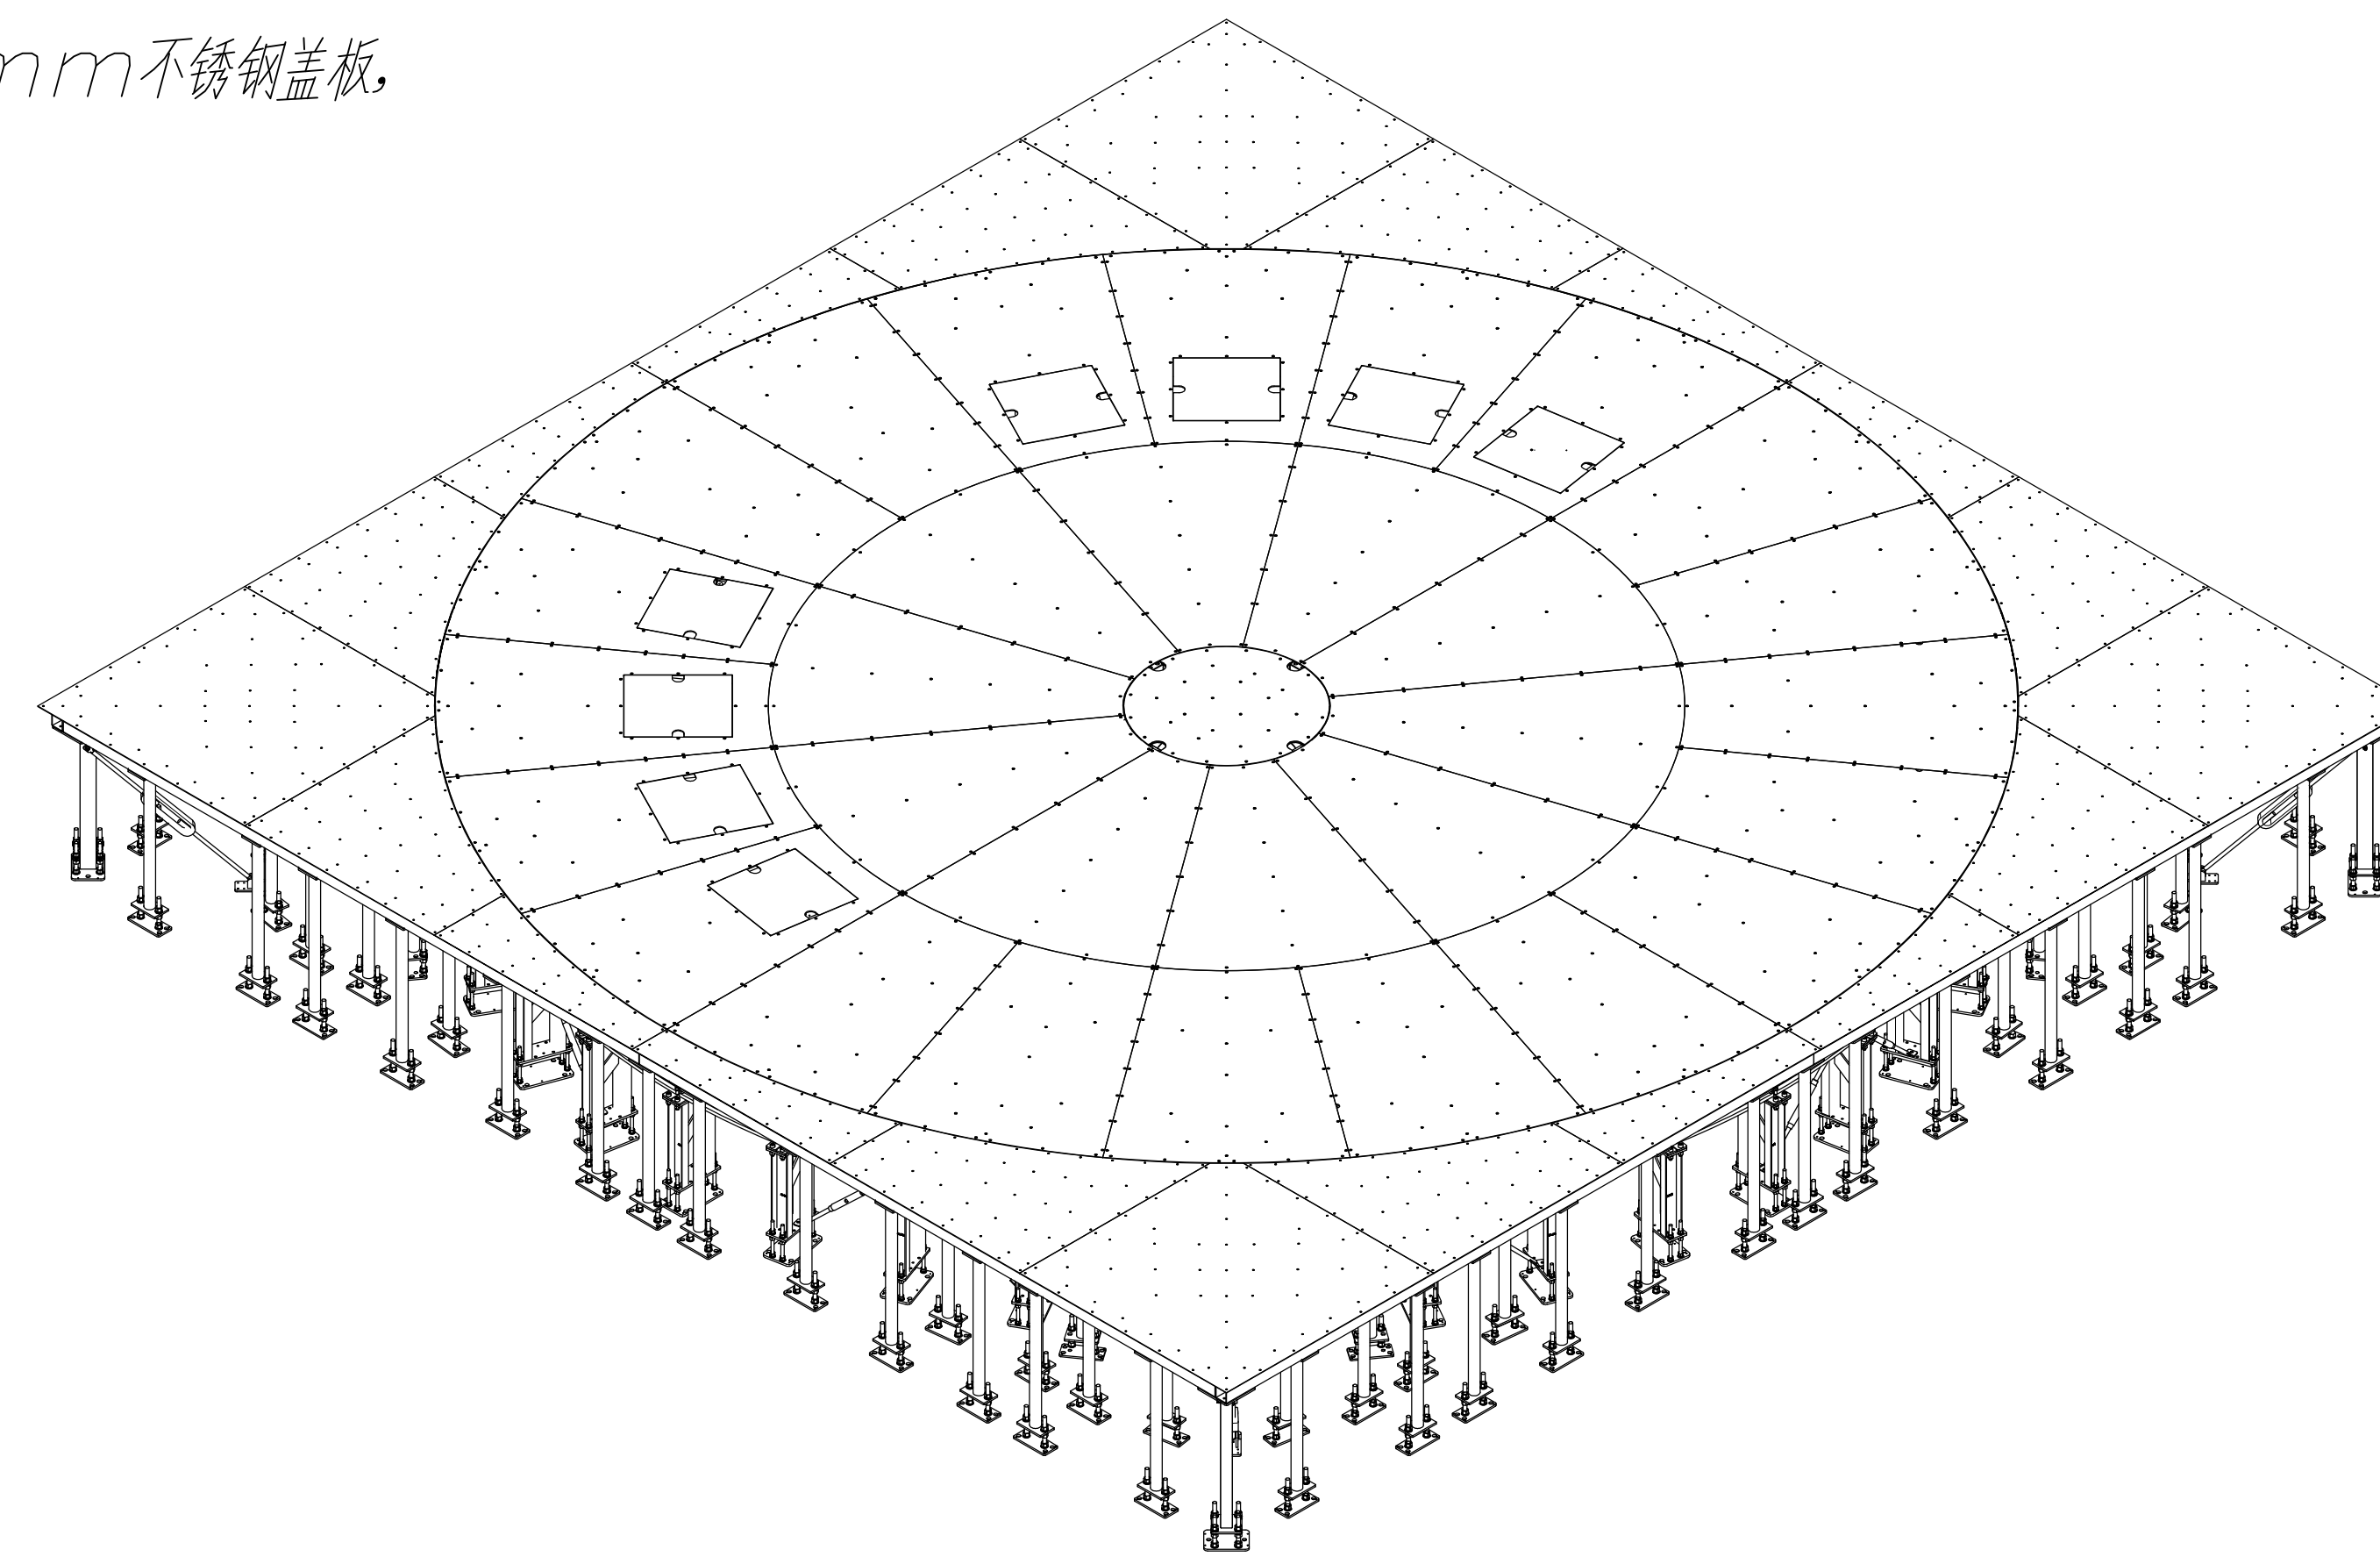

拖链进线口，预留铜排箱

柔性电缆170条；

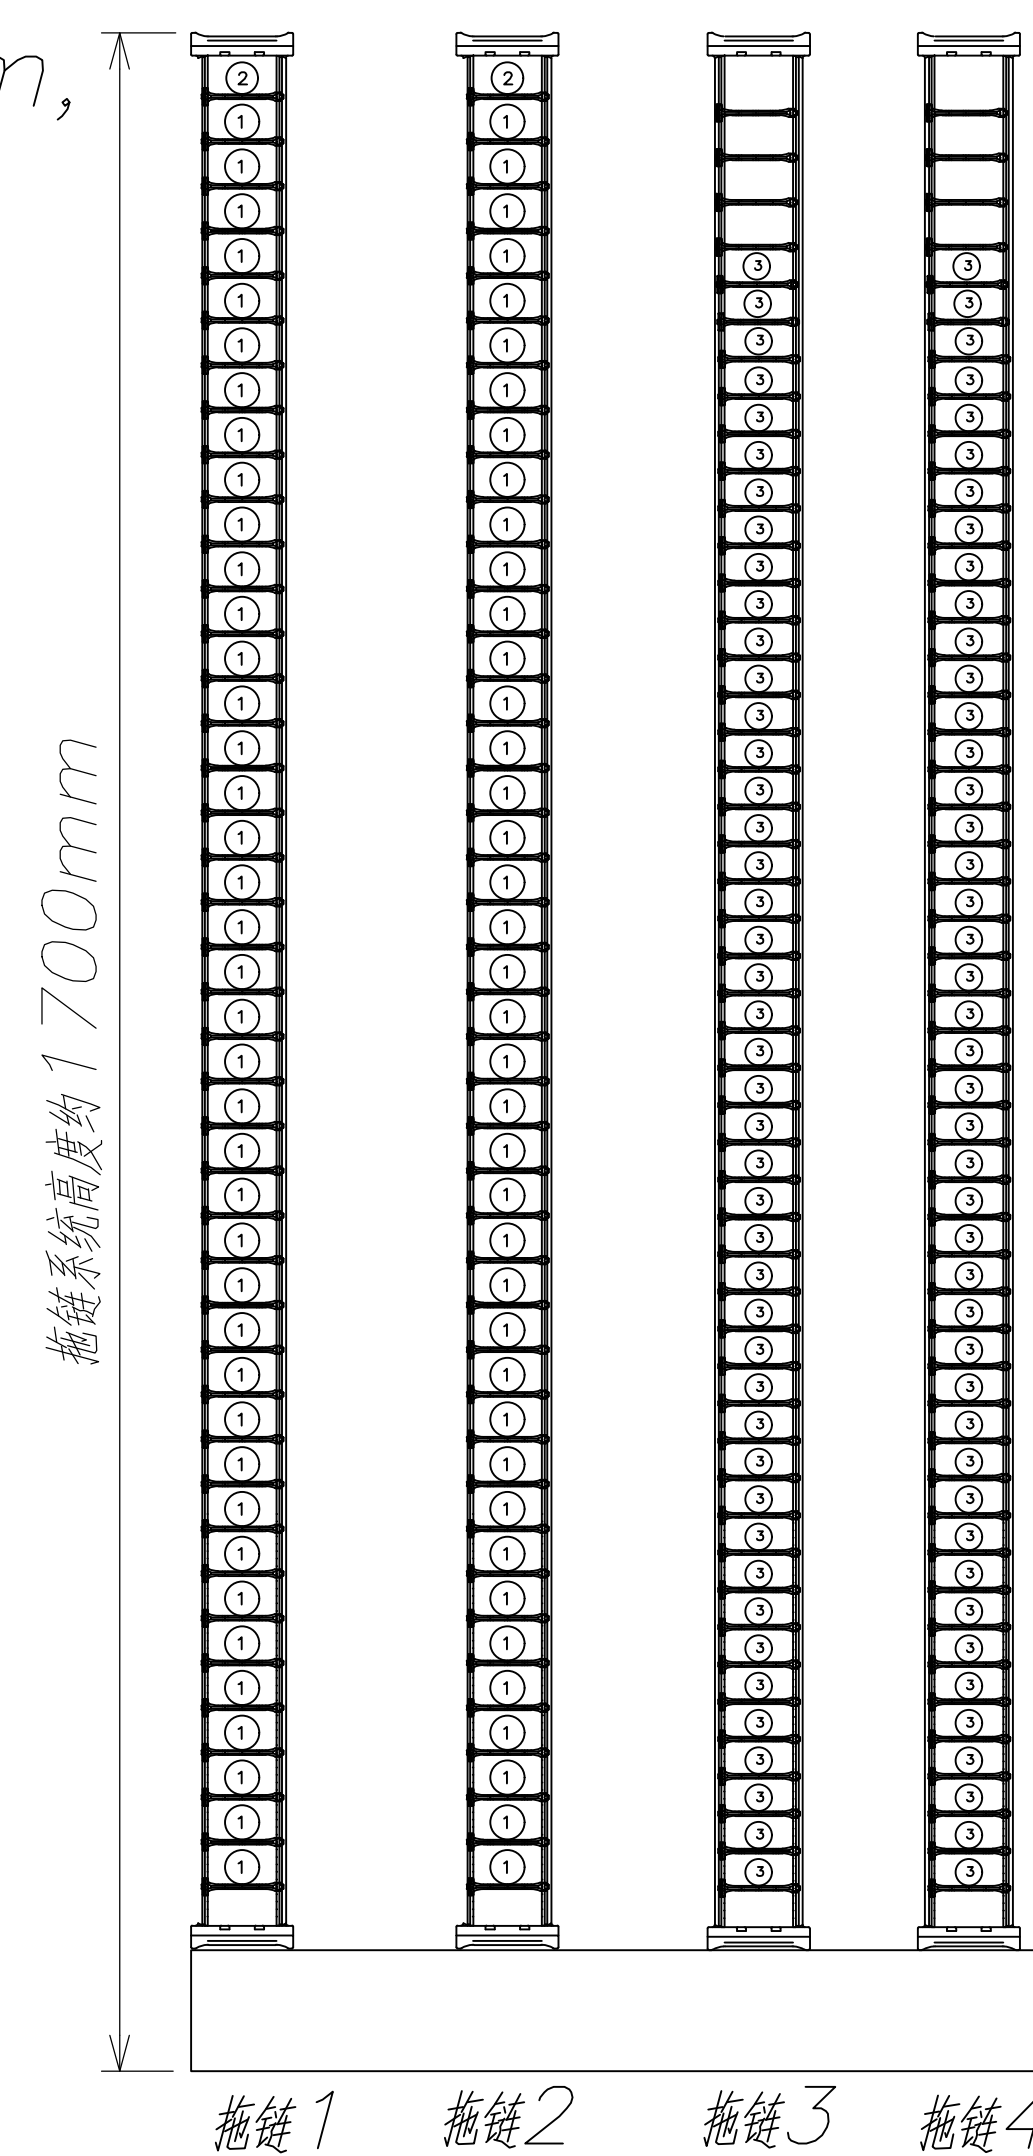

				图号				
				名 称	8米50吨转台内置拖链系统			
标记	处数	更改文件号	签 字	日期	产品名称	重量 (kg)		数量
设 计	XWL	日 期	12.29			比例		单位
制 图		日 期			产品编号	数 量	比 例	单 位
校 对		日 期				1	1:1	mm
审 核		日 期						版本号
								00